

DIARMUID WOLFE PORTFOLIO







Hand drawings depicting tone and spatiality









Test renders for hero weapon, to be heated over flame and used as brand



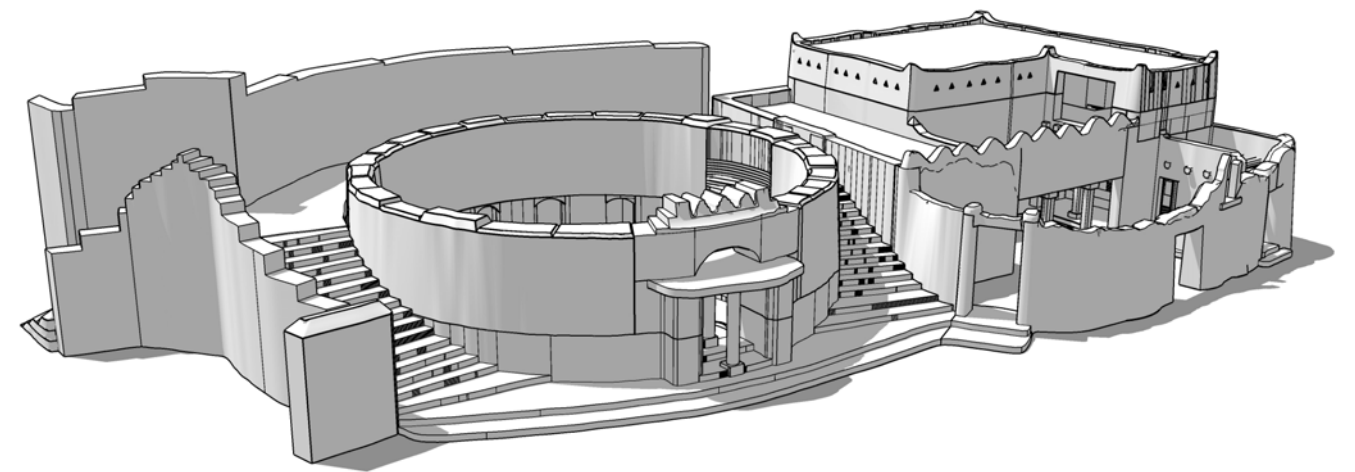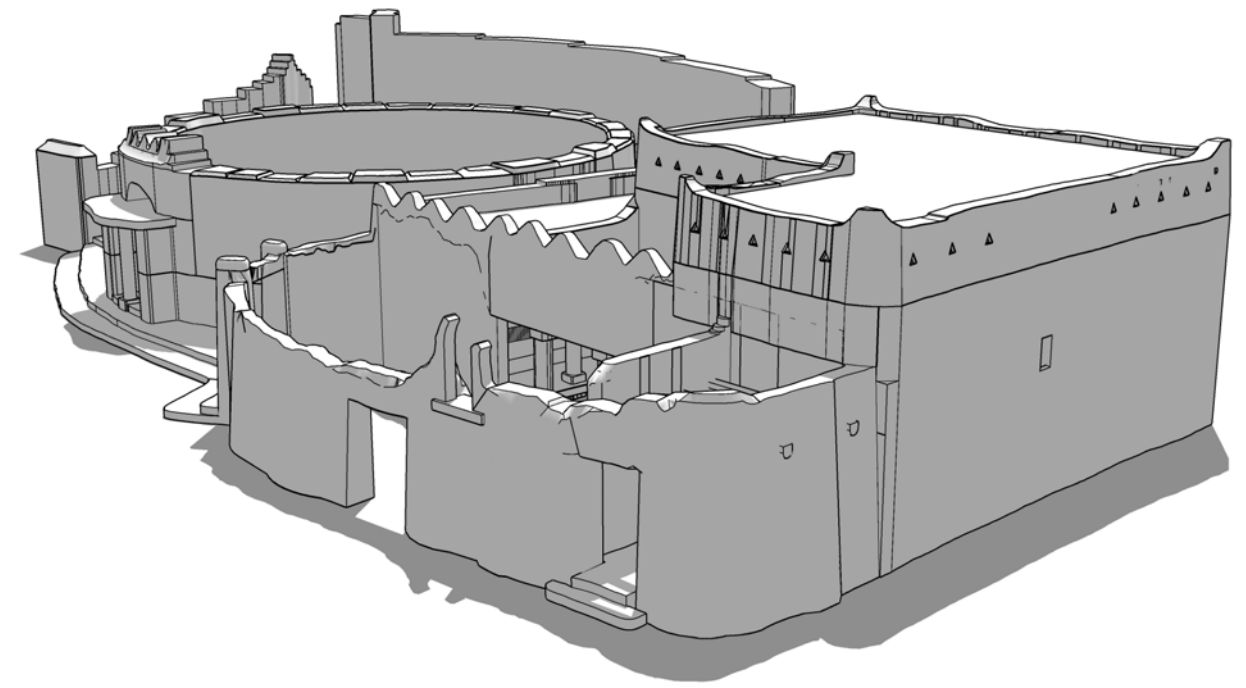

Left; Photographic collage, and Right subsequent 3d model built from Art Director's drawings. Model then converted and used by CNC machine to fabricate set



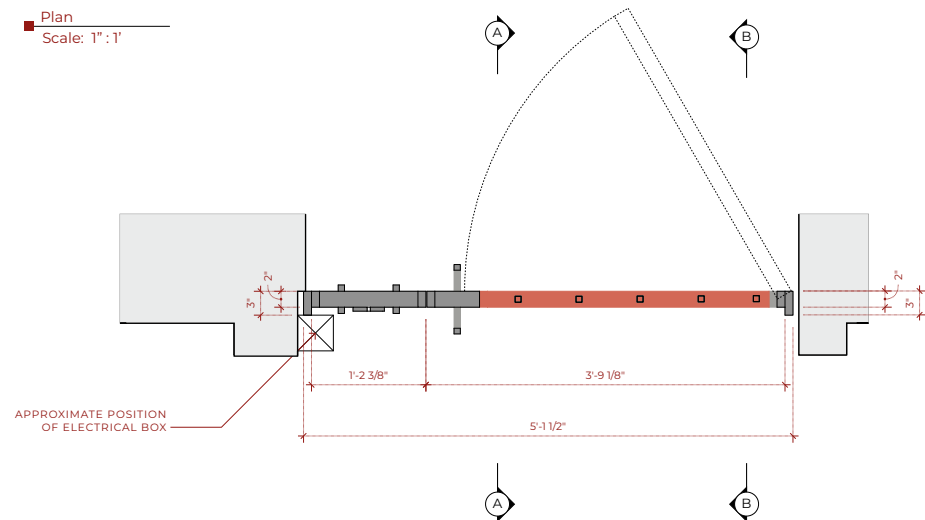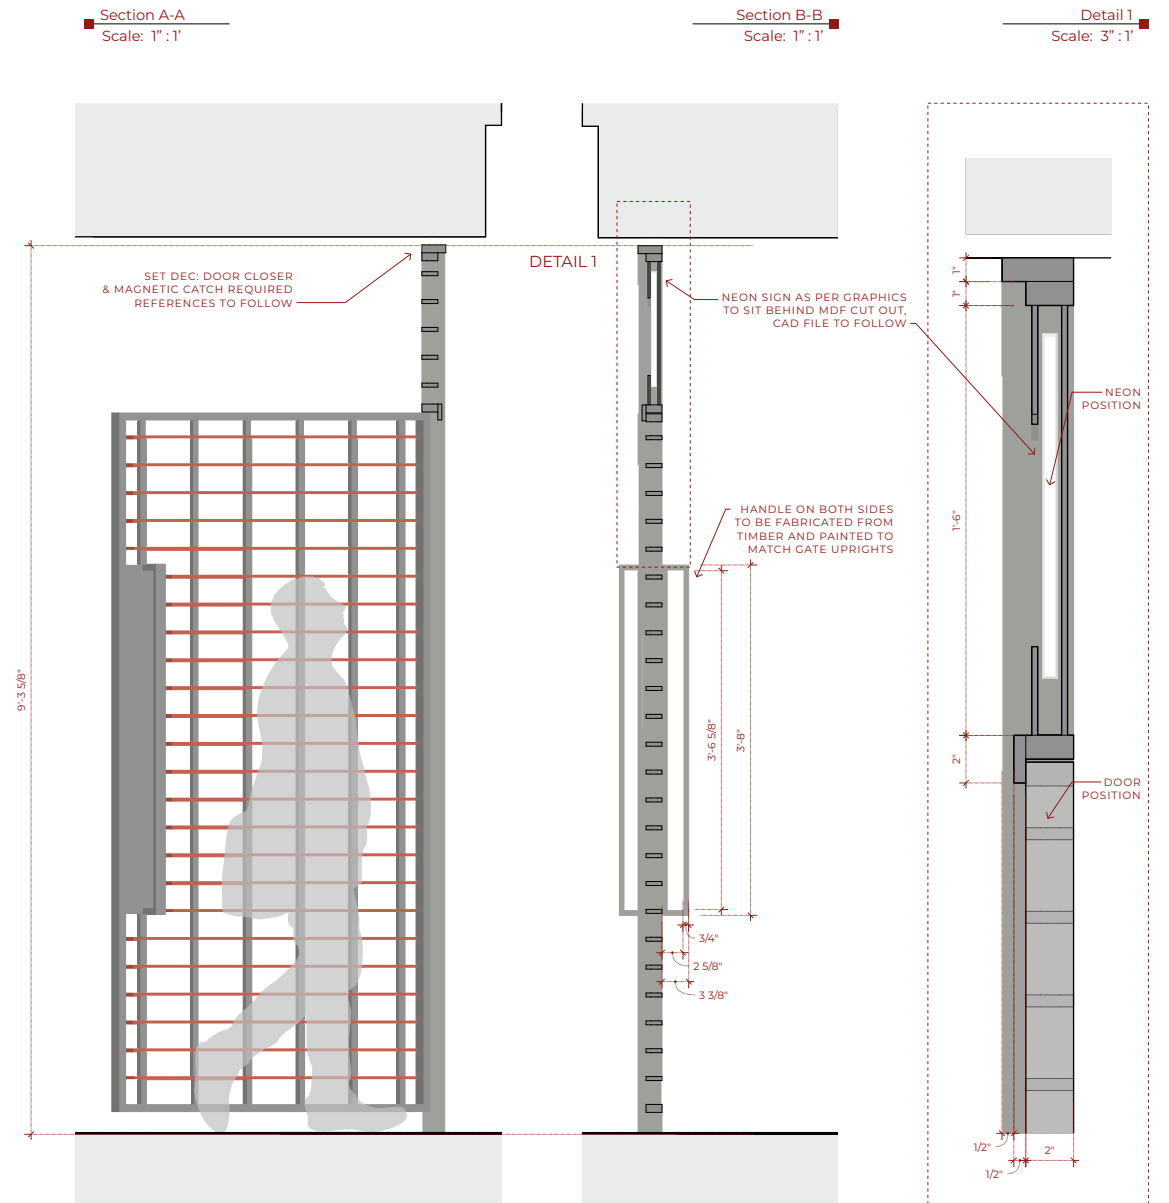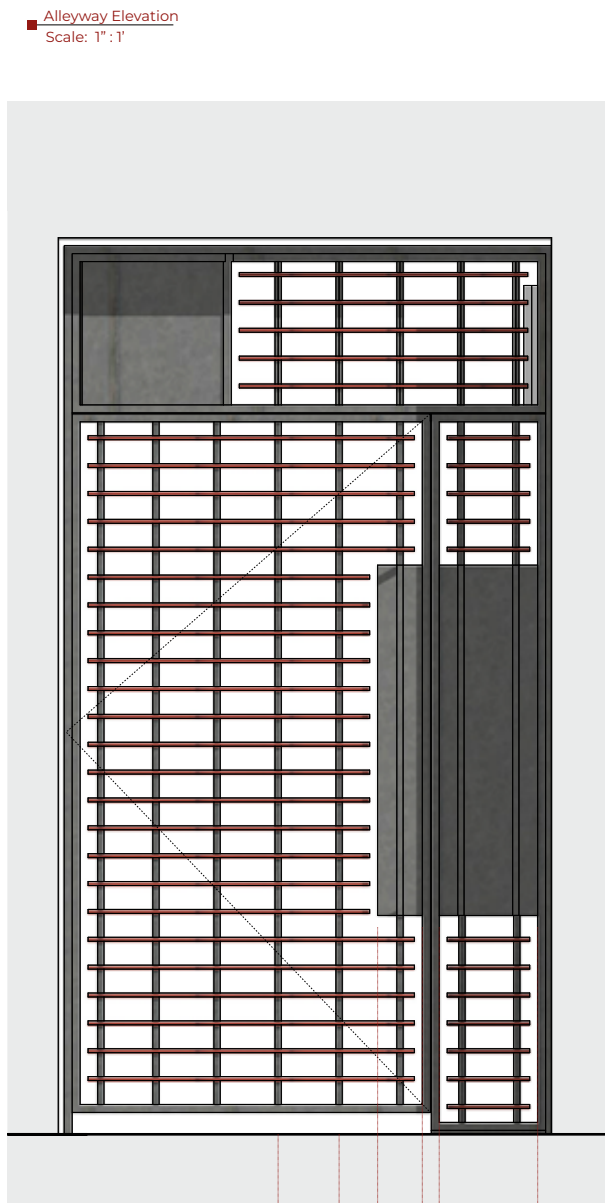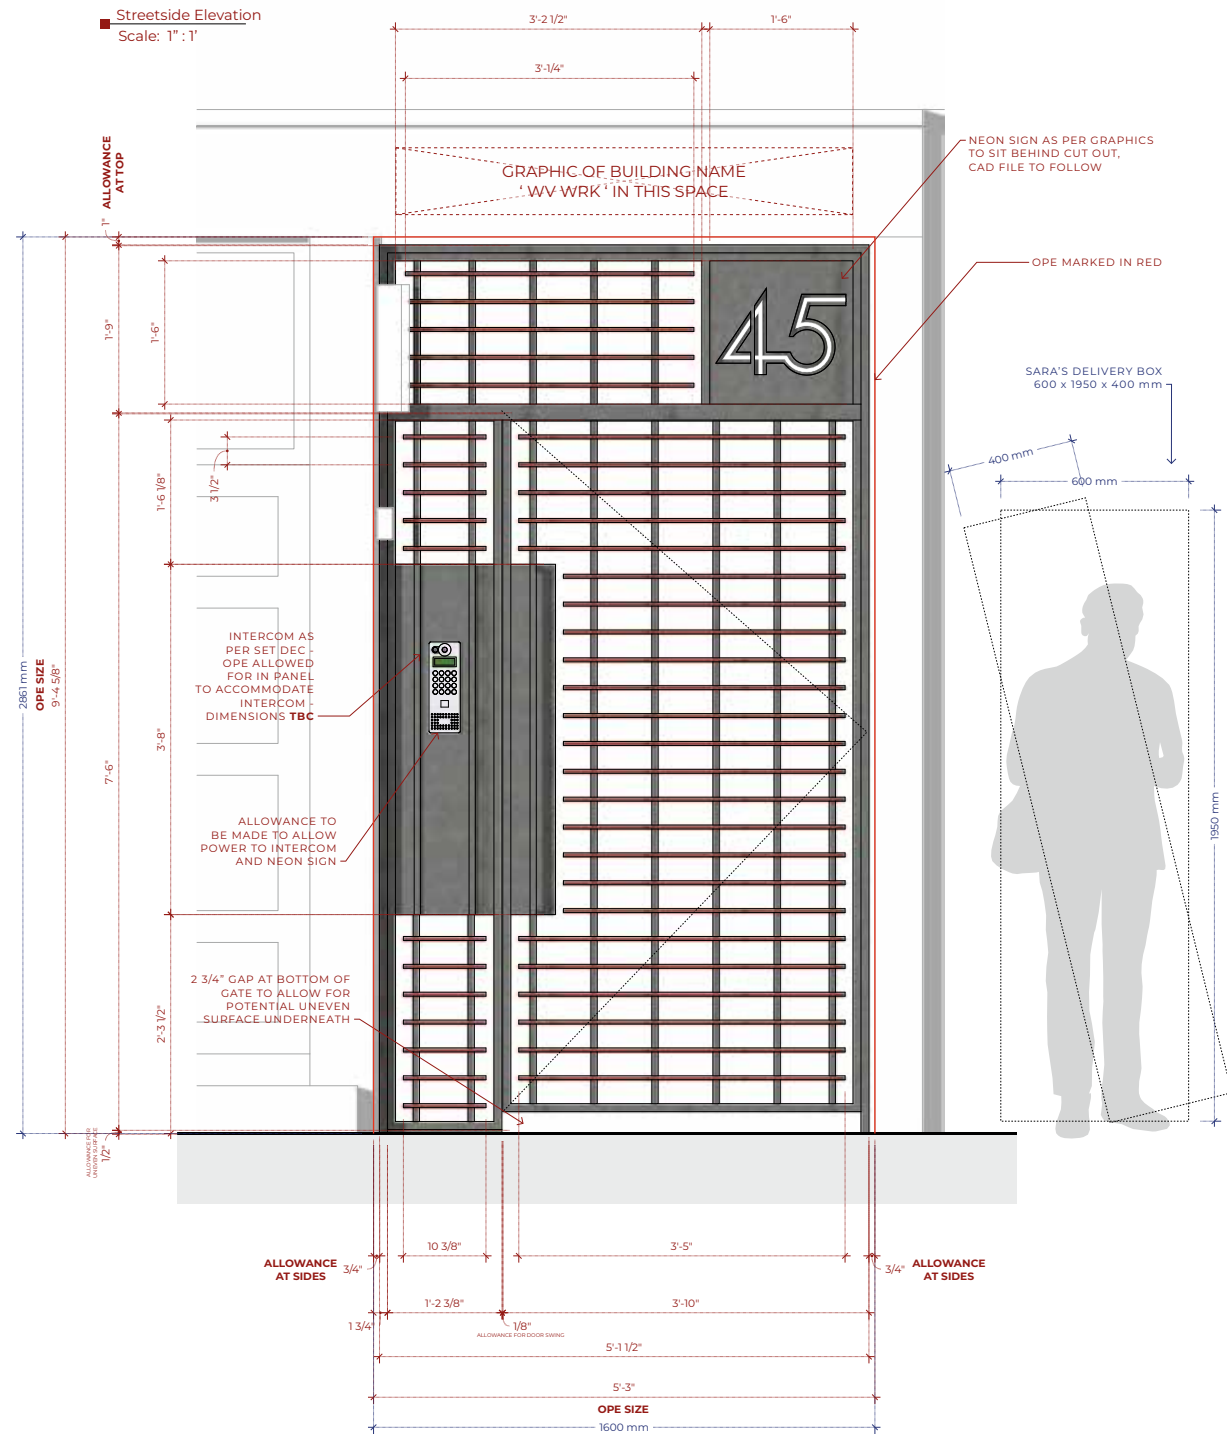

**Renders**  
Scale: NTS



**NB GENERAL:** METALWORKERS TO PROVIDE STEEL FRAME. HORIZONTAL ELEMENTS, PANEL FOR INTERCOM AND PANEL FOR NEON TO BE CONSTRUCTED FROM MDF / APPROPRIATE TIMBER AND PAINTED AS PER PRODUCTION DESIGNER.

**NB CONSTRUCTION:** METAL FINISHES AS PER PRODUCTION DESIGNER. PANELS TO BE MADE FOR INTERCOM & NEON SIGN. ALLOWANCE TO BE MADE TO ACCOMMODATE INTERCOM AND NEON SIGN EXACT SPECIFICATION AND DIMENSIONS TO FOLLOW.

**NB SET DEC:** INTERCOM AS PER REFERENCE. DOOR CLOSER REQUIRED AS PER REFERENCE TO FOLLOW. MAGNETIC DOOR CATCH REQUIRED REFERENCE TO FOLLOW.



**NB GRAPHICS:** NEON SIGN 'No. 45'. GRAPHIC OF BUILDING NAME 'VV WRK' APPLIED ABOVE GATE.

**NB PRAC SPARK:** ALLOWANCE TO BE MADE TO PROVIDE POWER TO INTERCOM & NEON SIGN - PREFERENCE DARK CABLE ON ALLEYWAY SIDE.




ISSUED 27.09.2024

| SOULM8TE                  |                   |             |  |                         |  |            | DESIGNER<br>SUSIE CULLEN |             |
|---------------------------|-------------------|-------------|--|-------------------------|--|------------|--------------------------|-------------|
| SET                       |                   |             |  |                         |  |            | DWG No.                  | 047         |
| EXT DAVID'S APARTMENT     |                   |             |  |                         |  |            | SET No.                  | 107         |
| DETAILS                   |                   |             |  |                         |  |            | SCALE                    | 1" : 1', FS |
| APRT. GATE - ESSEX STREET |                   |             |  |                         |  |            |                          |             |
| DRAWN BY                  | DW                | PRODUCER    |  | DECORATOR               |  | CON. MNGR  | CAMERA                   | VFX         |
| APPROVED                  | BT                | DIRECTOR    |  | BUYER                   |  | CARPENTERS | GAFFER                   | SFX         |
| DATE DRAWN                | 11.09.2024        | PRODUCTION  |  | PROPS                   |  | PLASTERERS | METAL                    | ART         |
| DATE ISSUED               | 27.09.2024        | LOCATIONS   |  | DRAPES                  |  | PAINTERS   | RIGGERS                  | GFX         |
| LOCATION                  | ESSEX ST., DUBLIN | MODELMAKERS |  | CONSTRUCTION MODELMAKER |  | STUNTS     | GREENS                   |             |







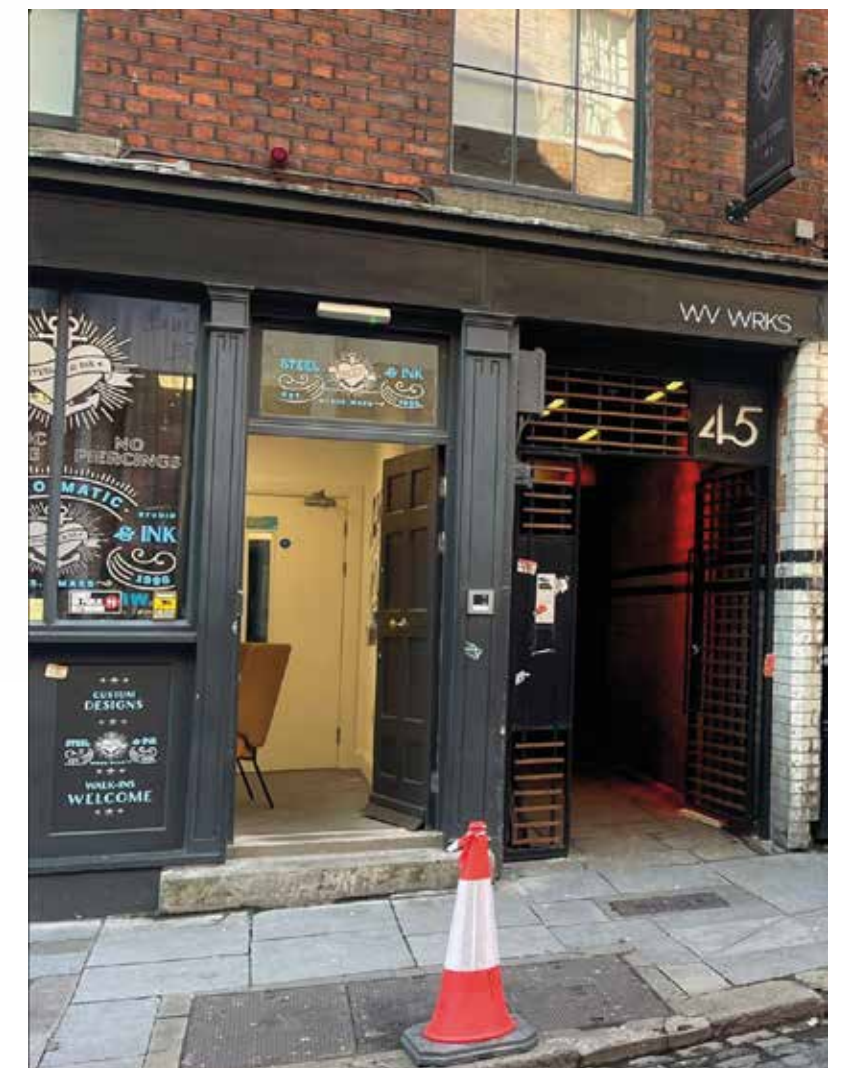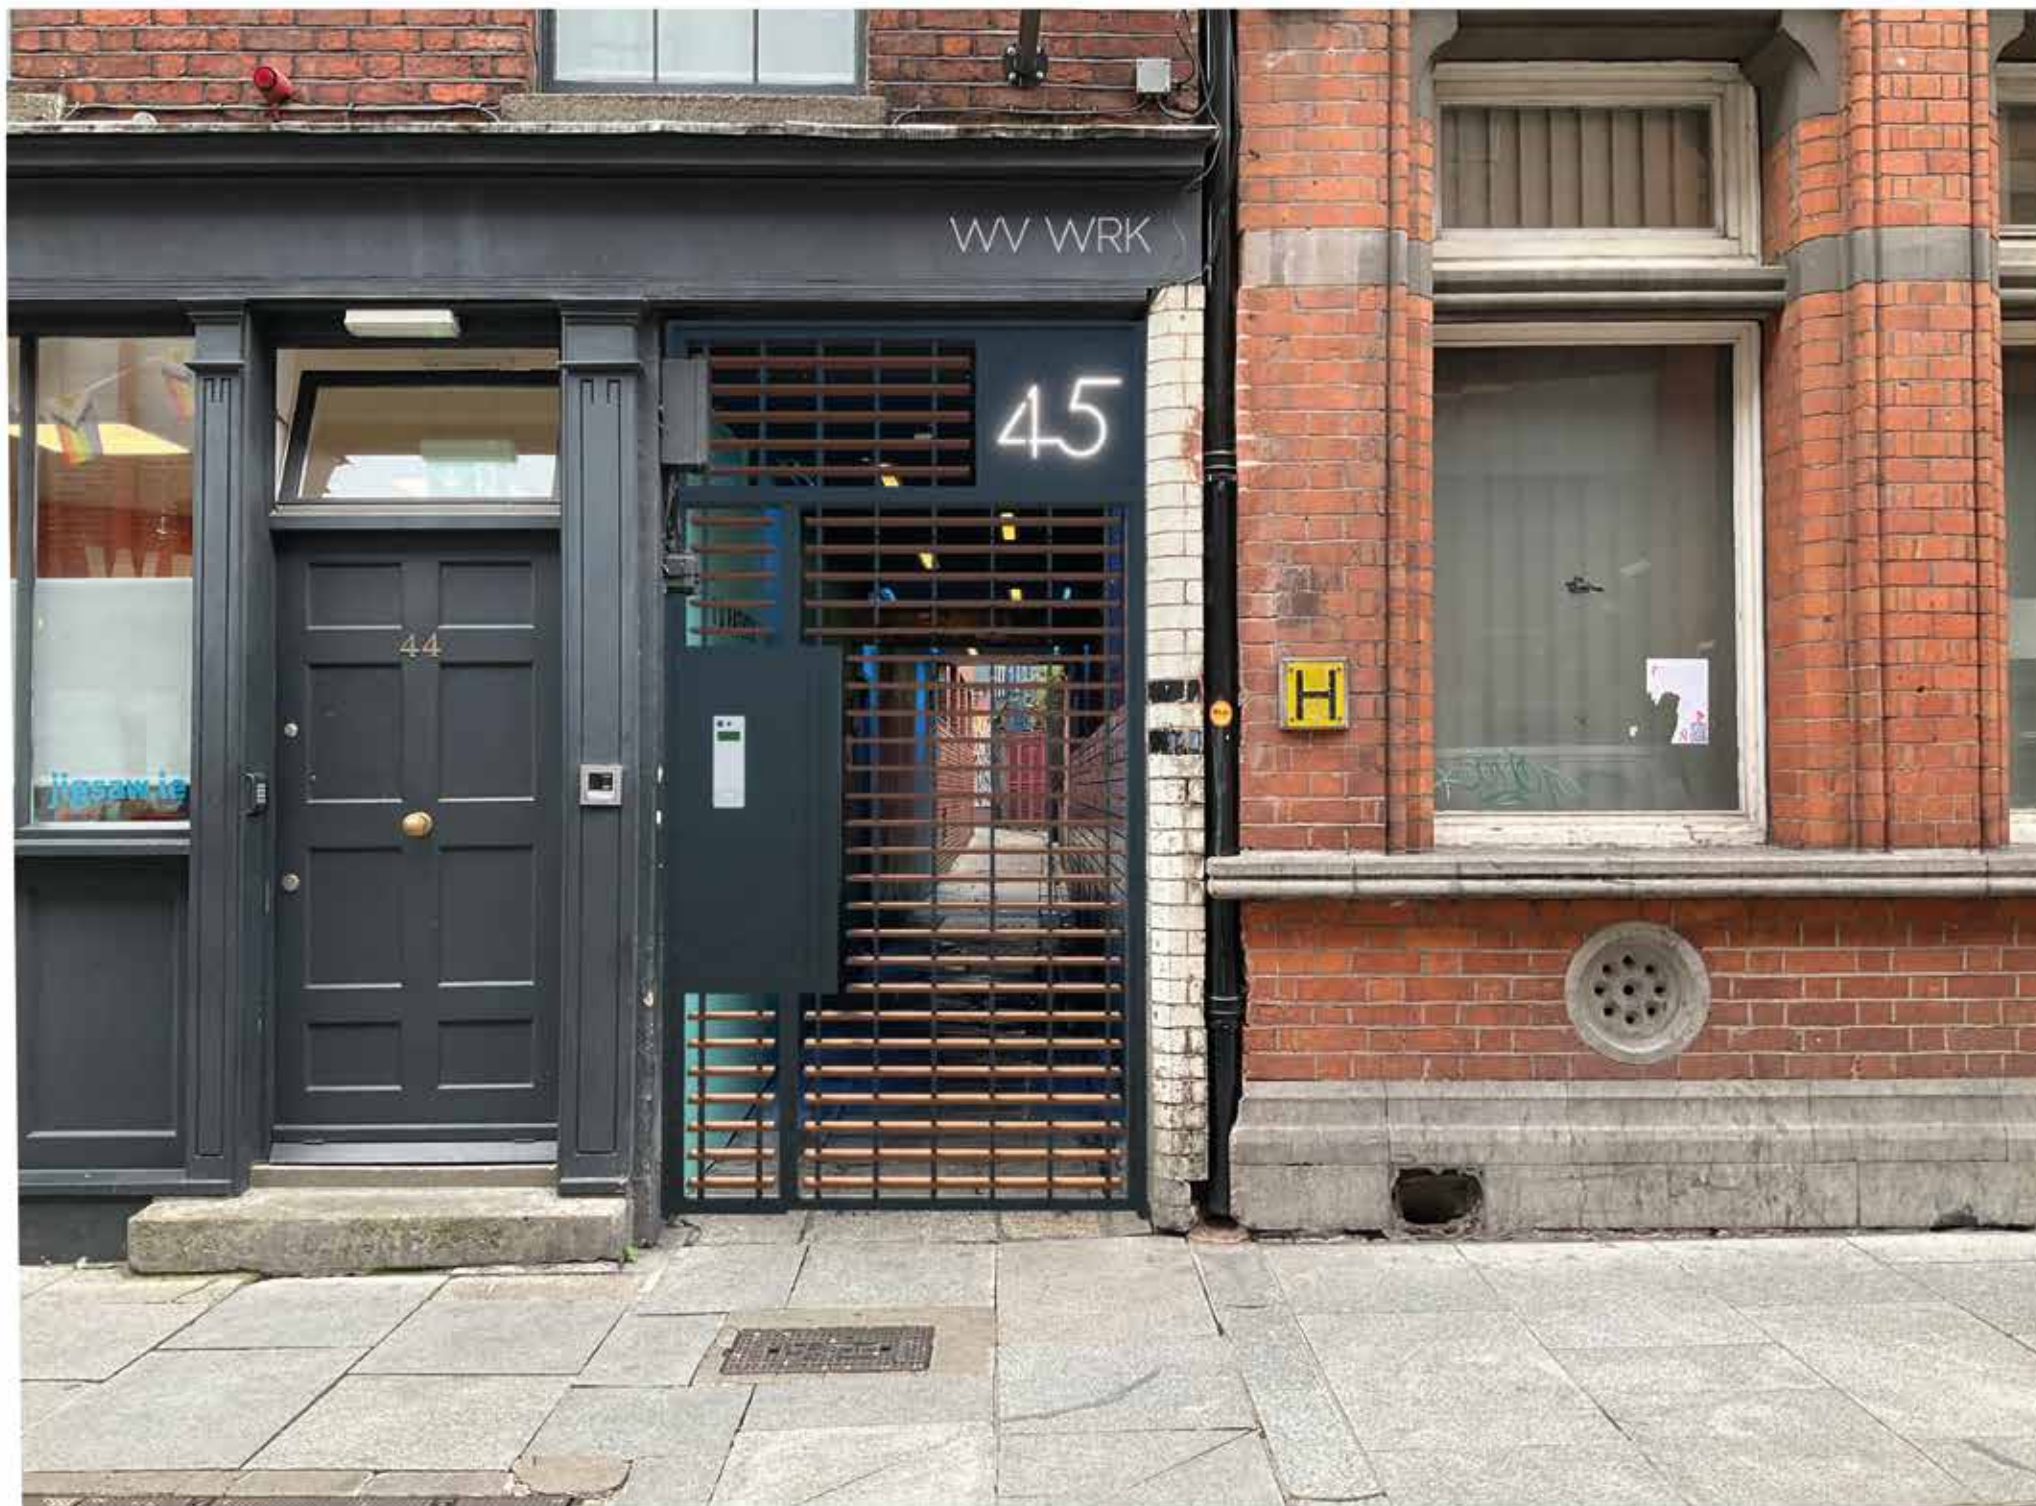







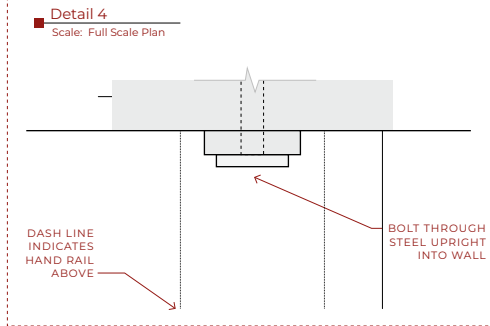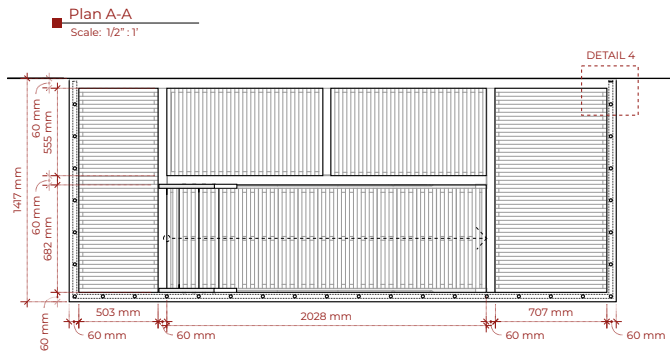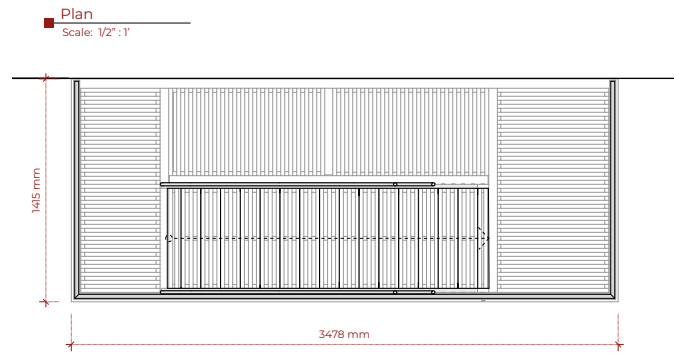

Reference  
Scale: NTS

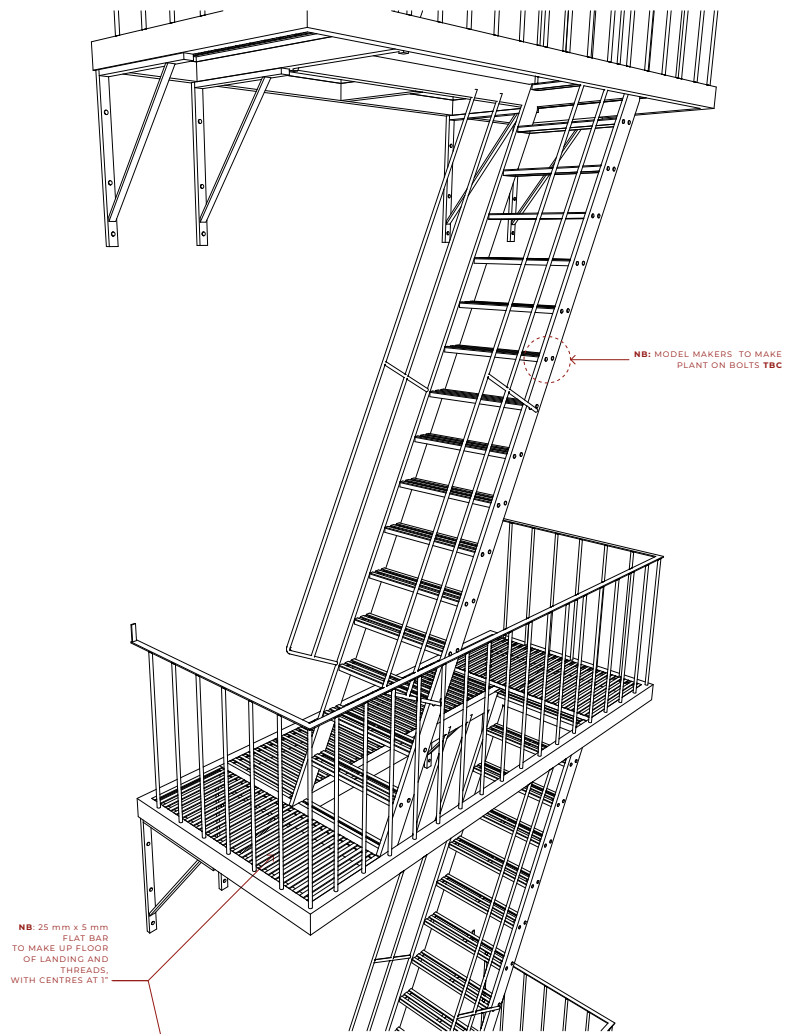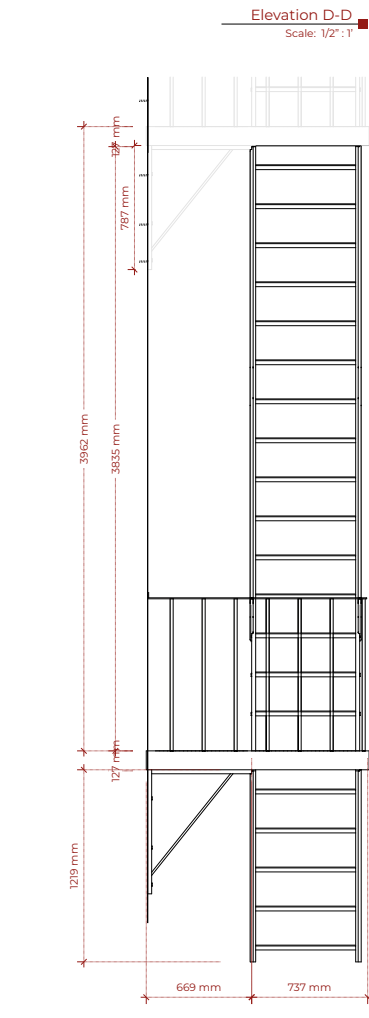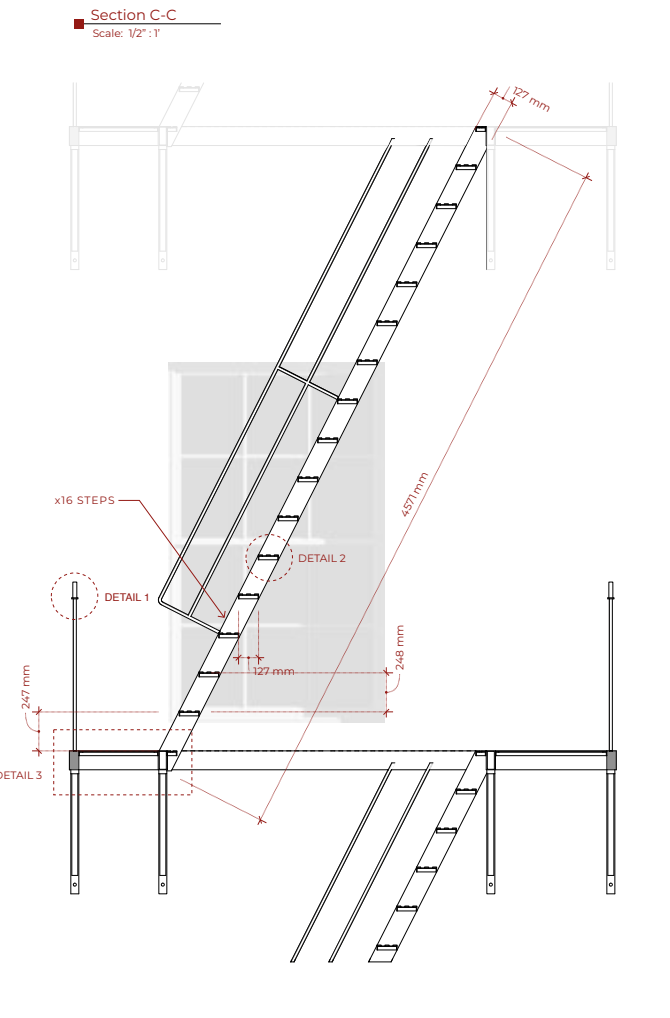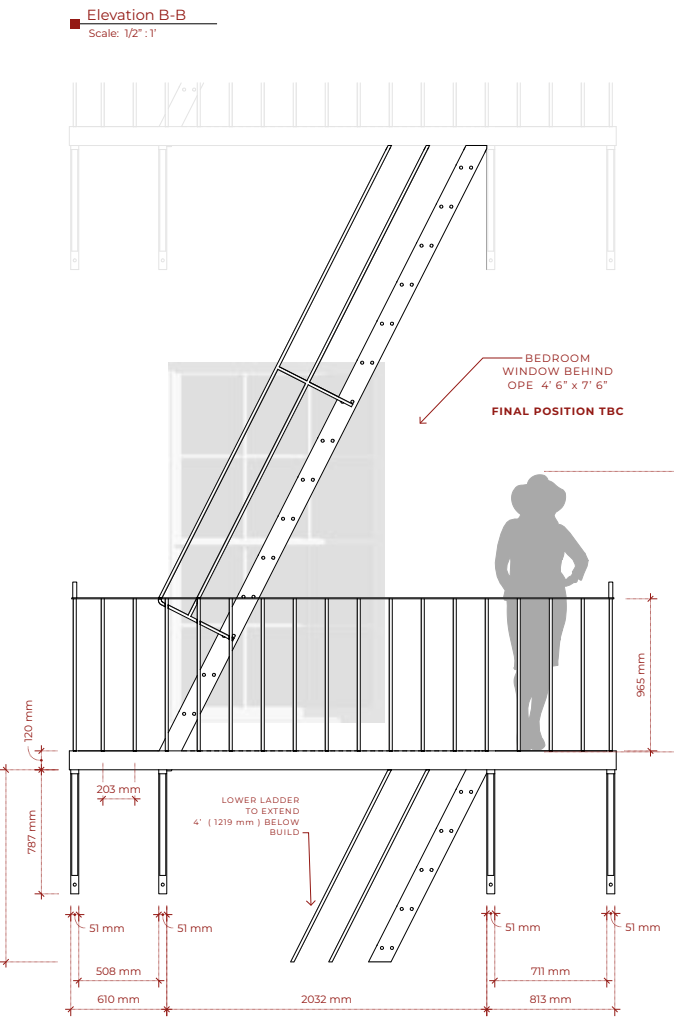

Reference  
Scale: NTS

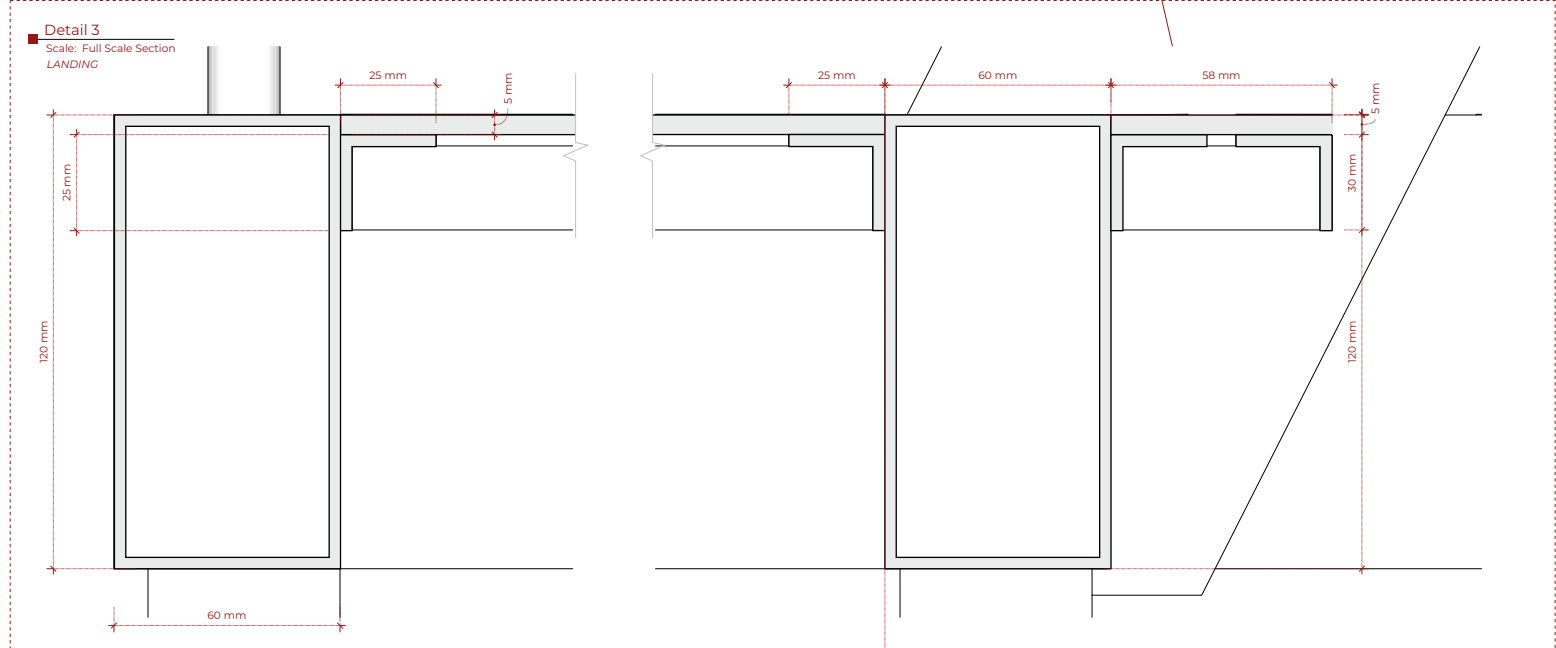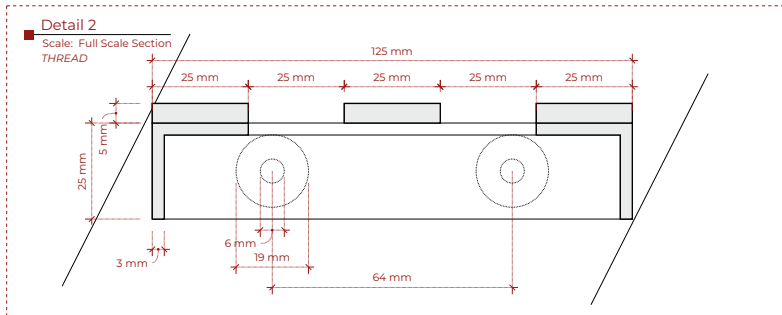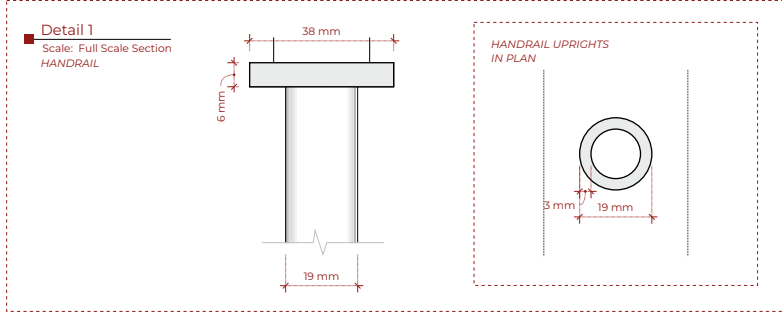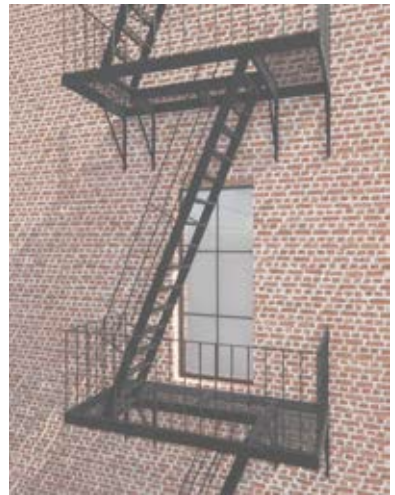

NB: MODEL MAKERS TO MAKE PLANT ON BOLTS TBC


METRIC DIMENSIONS  
ISSUED 22.08.2024

| SOULMØTE    |            |                    |   |              |   |             |   |         |   | DESIGNER<br>SUSIE CULLEN |               |
|-------------|------------|--------------------|---|--------------|---|-------------|---|---------|---|--------------------------|---------------|
| SET         |            | DAVID'S APT.       |   |              |   |             |   |         |   | DWG No.                  | 006           |
| DETAILS     |            | FIRE ESCAPE DETAIL |   |              |   |             |   |         |   | SET No.                  | 112           |
|             |            |                    |   |              |   |             |   |         |   | SCALE                    | 1/2" : 1', FS |
| DRAWN BY    | DW         | PRODUCER           | X | DECORATOR    | X | CON. MNGR   | X | CAMERA  | X | VFX                      | X             |
| APPROVED    |            | DIRECTOR           | X | BUYER        | X | CARPENTERS  | X | GAFFER  | X | SFX                      | X             |
| DATE DRAWN  | 06.08.2024 | PRODUCTION         |   | PROPS        | X | PLASTERERS  | X | METAL   | X | ART                      | X             |
| DATE ISSUED | 22.08.2024 | LOCATIONS          | X | DRAPES       |   | PAINTERS    | X | RIGGERS | X | GFX                      |               |
| LOCATION    | A STAGE    | MODELMAKERS        |   | CONSTRUCTION |   | MODELMAKERS |   | STUNTS  |   | GREENS                   |               |




Elevation A-A  
Scale: 1"=1'


INSIDE

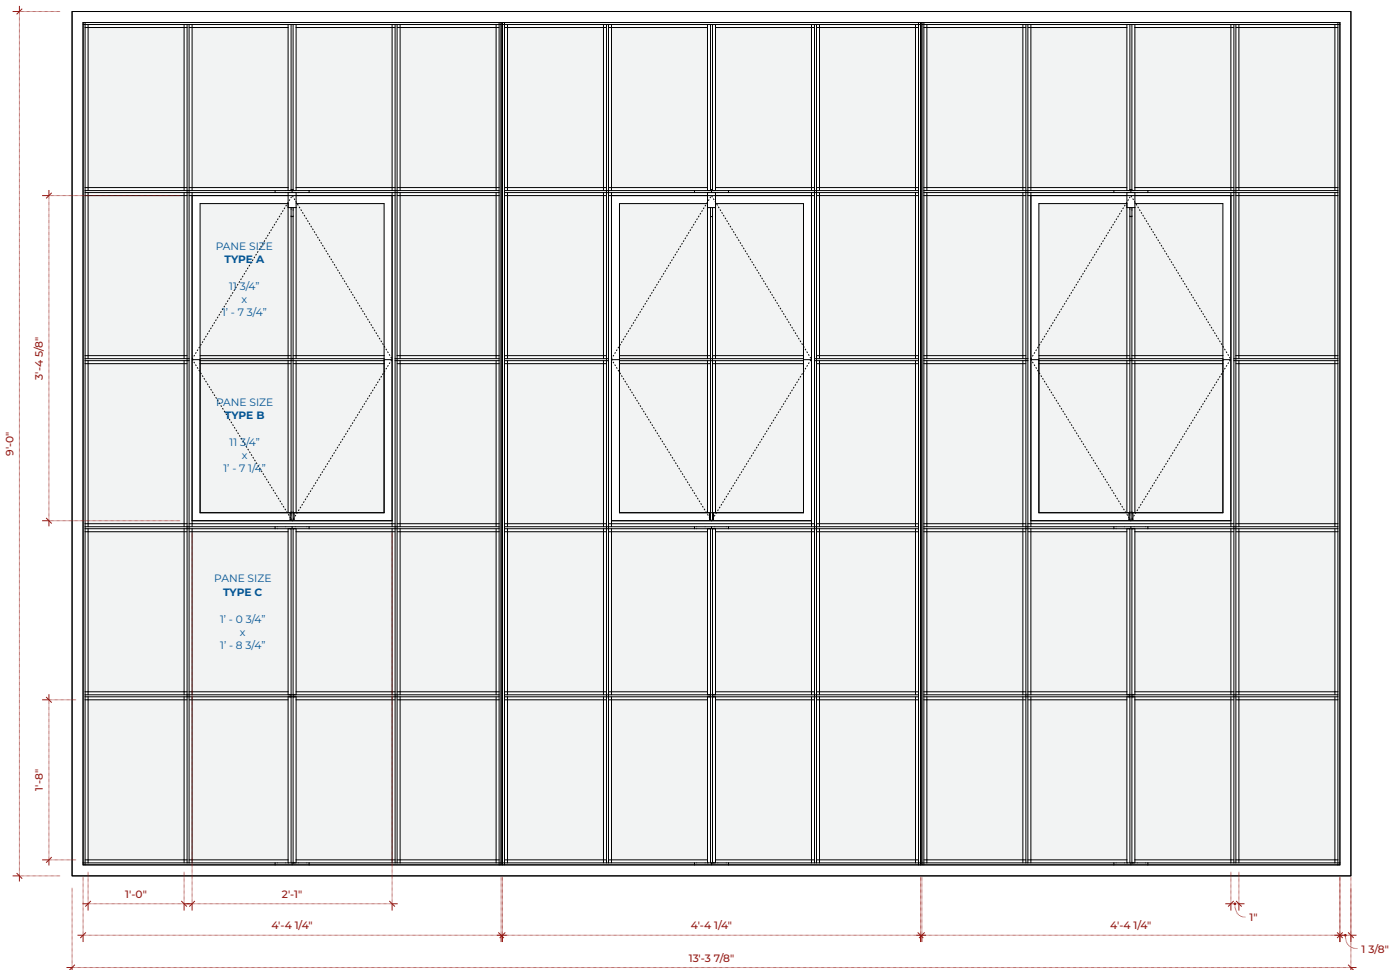


Plan  
Scale: 1"=1'

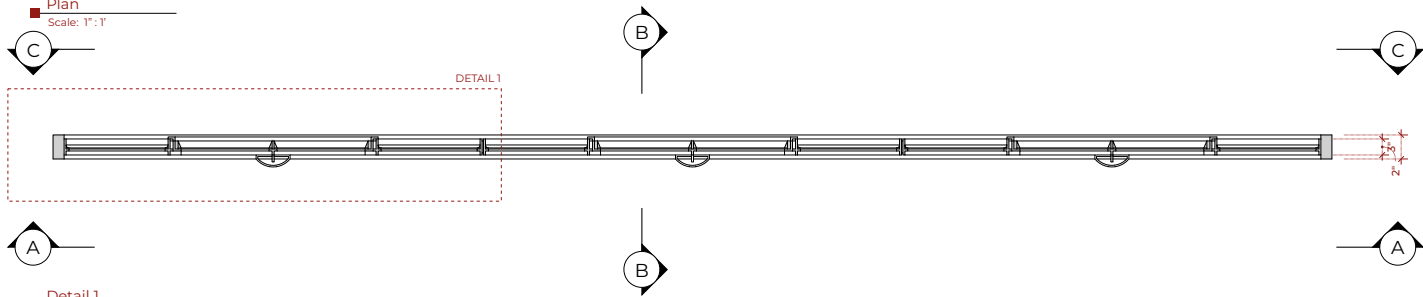


Detail 1  
Scale: 3"=1'

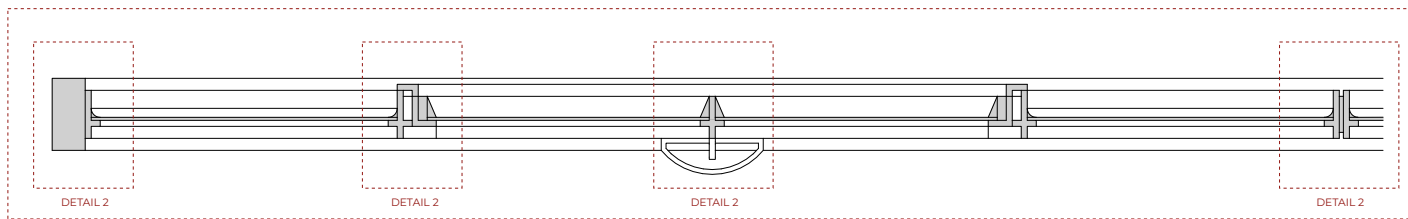

Detail 2  
Scale: Full Scale

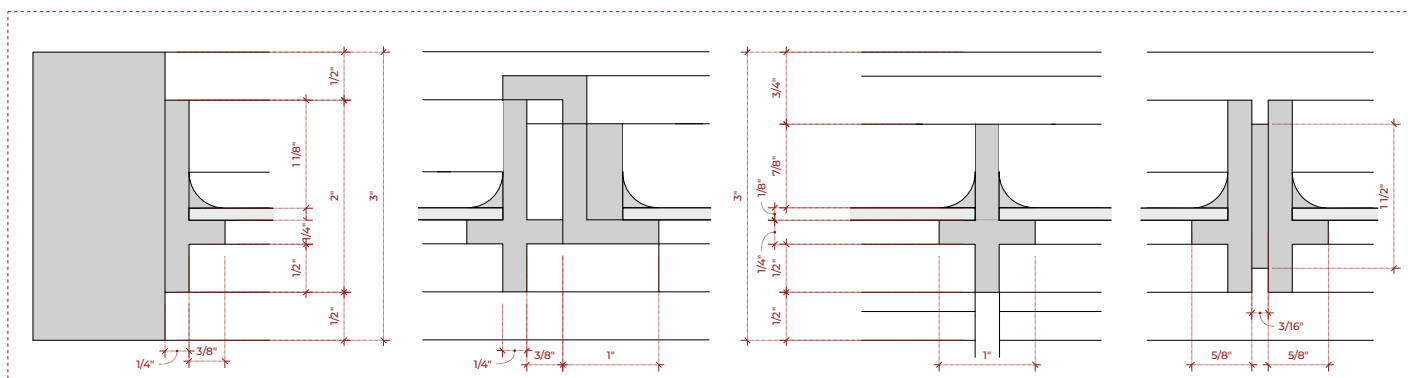

Section B-B  
Scale: 1"=1'

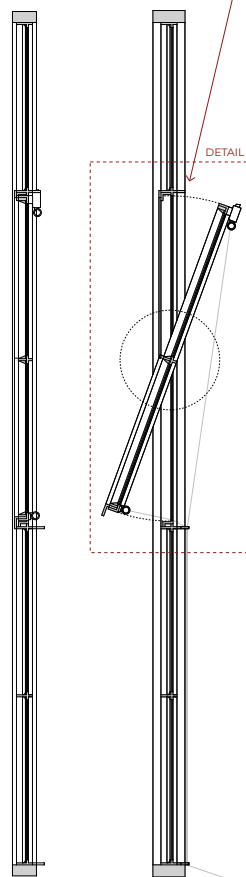


WINDOWS TO PIVOT;  
EXACT MECHANISM TBD


DETAIL 3

OUTSIDE

Elevation C-C  
Scale: 1"=1'

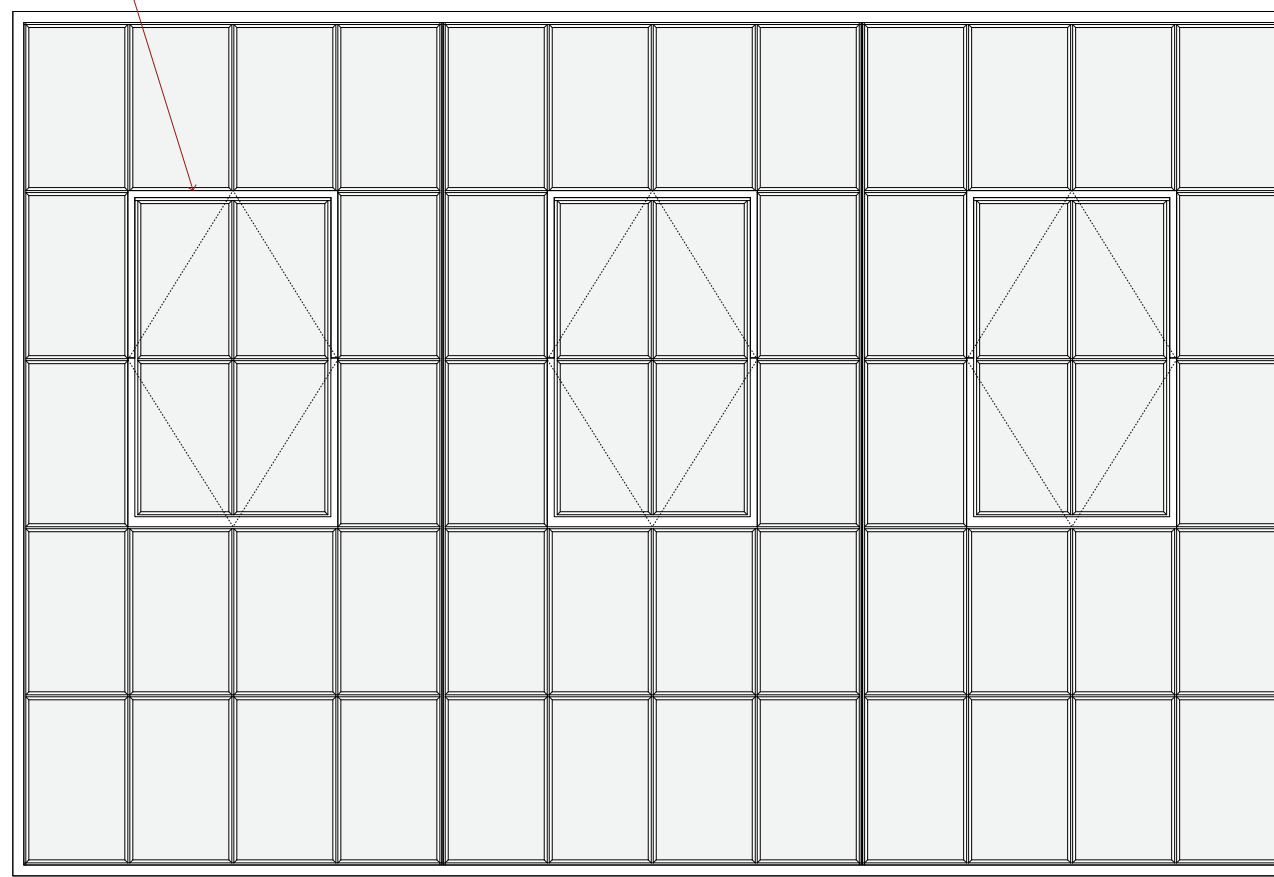


Detail 3  
Scale: 3"=1'

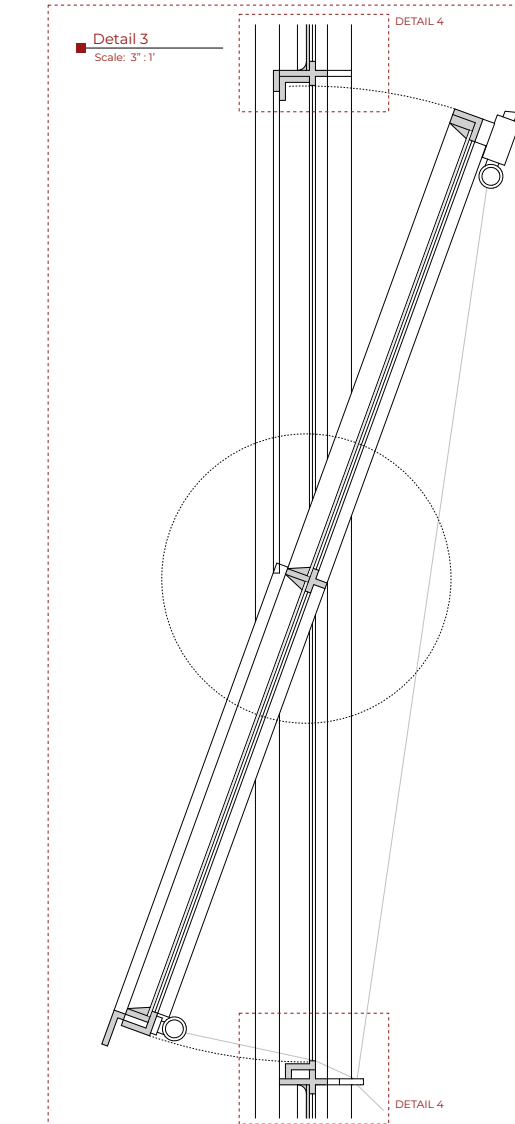


DETAIL 4

Detail 4  
Scale: Full Scale

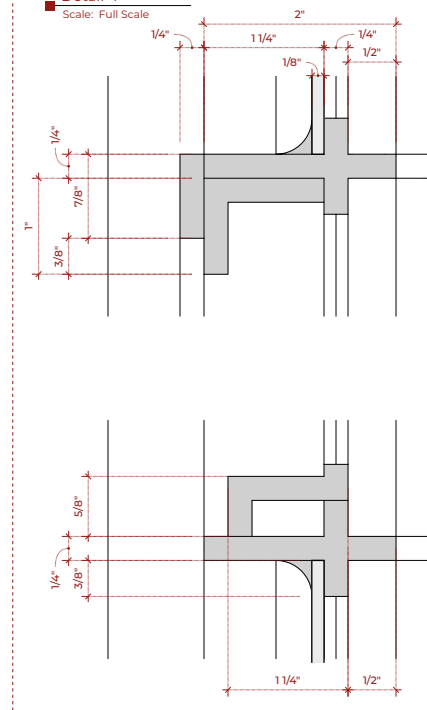

REFERENCE FOR PIVOT DETAIL

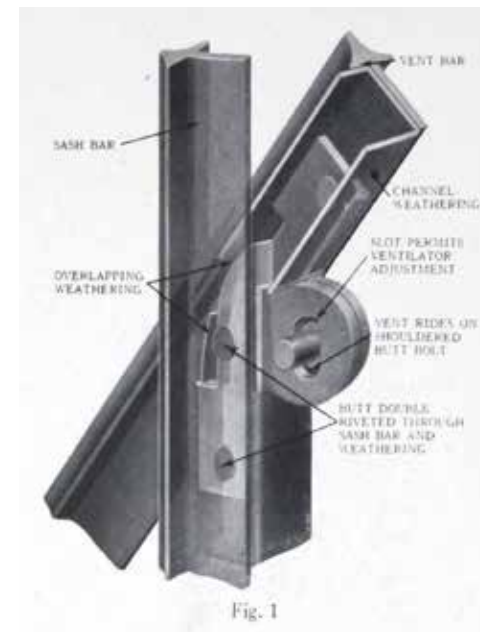

ISSUED 04.09.2024

GLASS PANE SCHEDULE

| TYPE | DIMS (W x H)            | QUANTITY |
|------|-------------------------|----------|
| A    | 11 3/4" x 1' - 7 3/4"   | x12      |
| B    | 11 3/4" x 1' - 7 1/4"   | x12      |
| C    | 1' - 0 3/4" x 1' 8 3/4" | x96      |

SOULMØTE

DESIGNER  
SUSIE CULLEN



DWG No. 023

SET No. 111

SCALE 1"=1', 3/4"=1', FS

| SET         | DAVID'S APT.  |             |              |            |         |        |
|-------------|---------------|-------------|--------------|------------|---------|--------|
| DETAILS     | WINDOW DETAIL |             |              |            |         |        |
| DRAWN BY    | DW            | PRODUCER    | DECORATOR    | CON. MNGR  | CAMERA  | VFX    |
| APPROVED    | SC            | DIRECTOR    | BUYER        | CARPENTERS | GAFFER  | SFX    |
| DATE DRAWN  | 12.08.2024    | PRODUCTION  | PROPS        | PLASTERERS | METAL   | ART    |
| DATE ISSUED | 04.09.2024    | LOCATIONS   | DRAPES       | PAINTERS   | RIGGERS | GFX    |
| LOCATION    | A STAGE       | MODELMAKERS | CONSTRUCTION | MODULAR    | STUNTS  | GREENS |



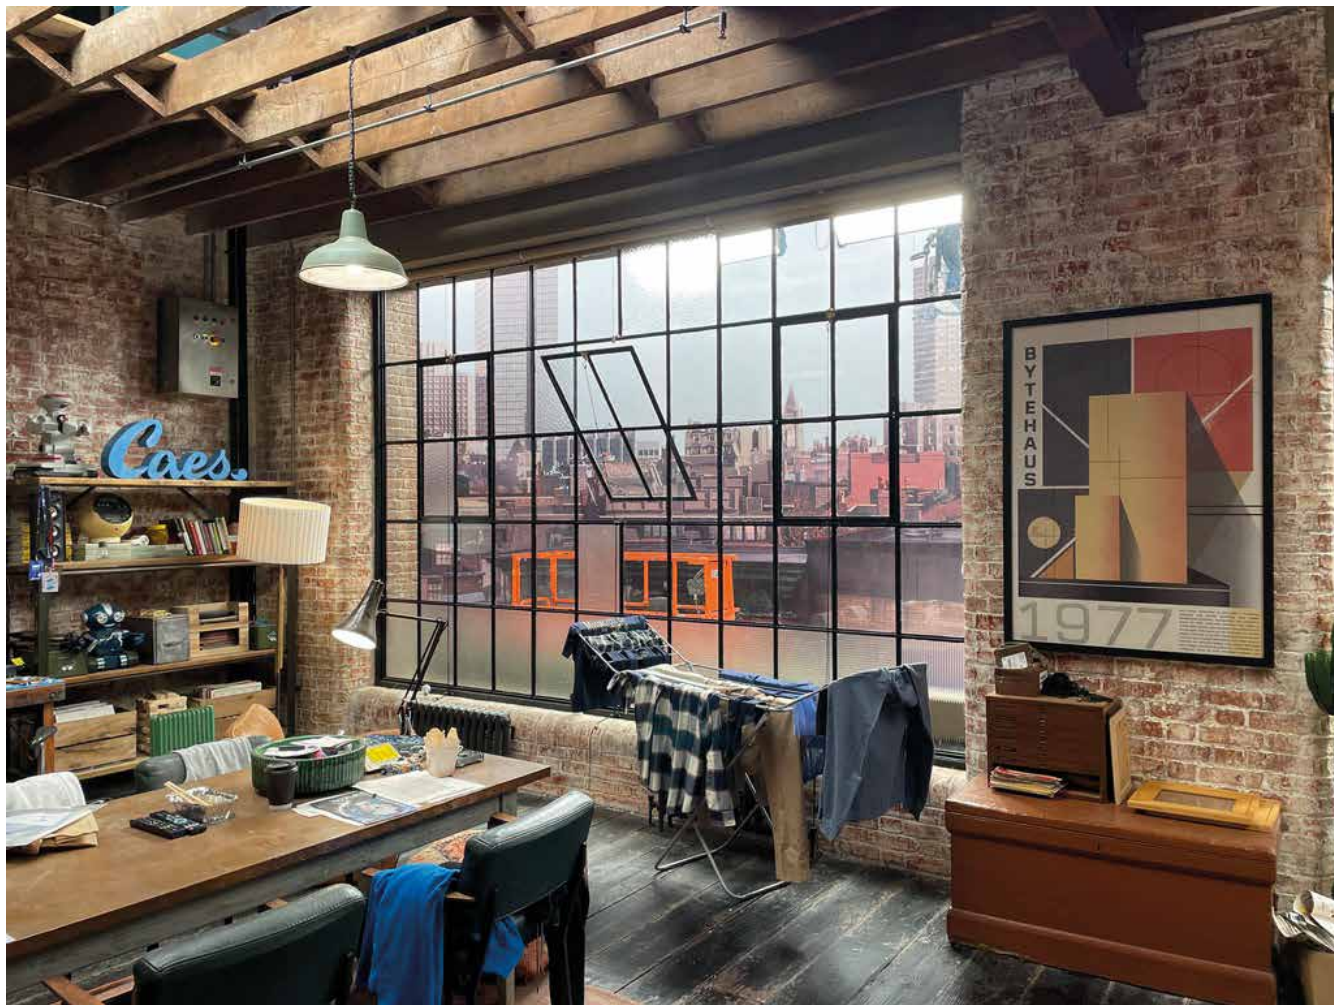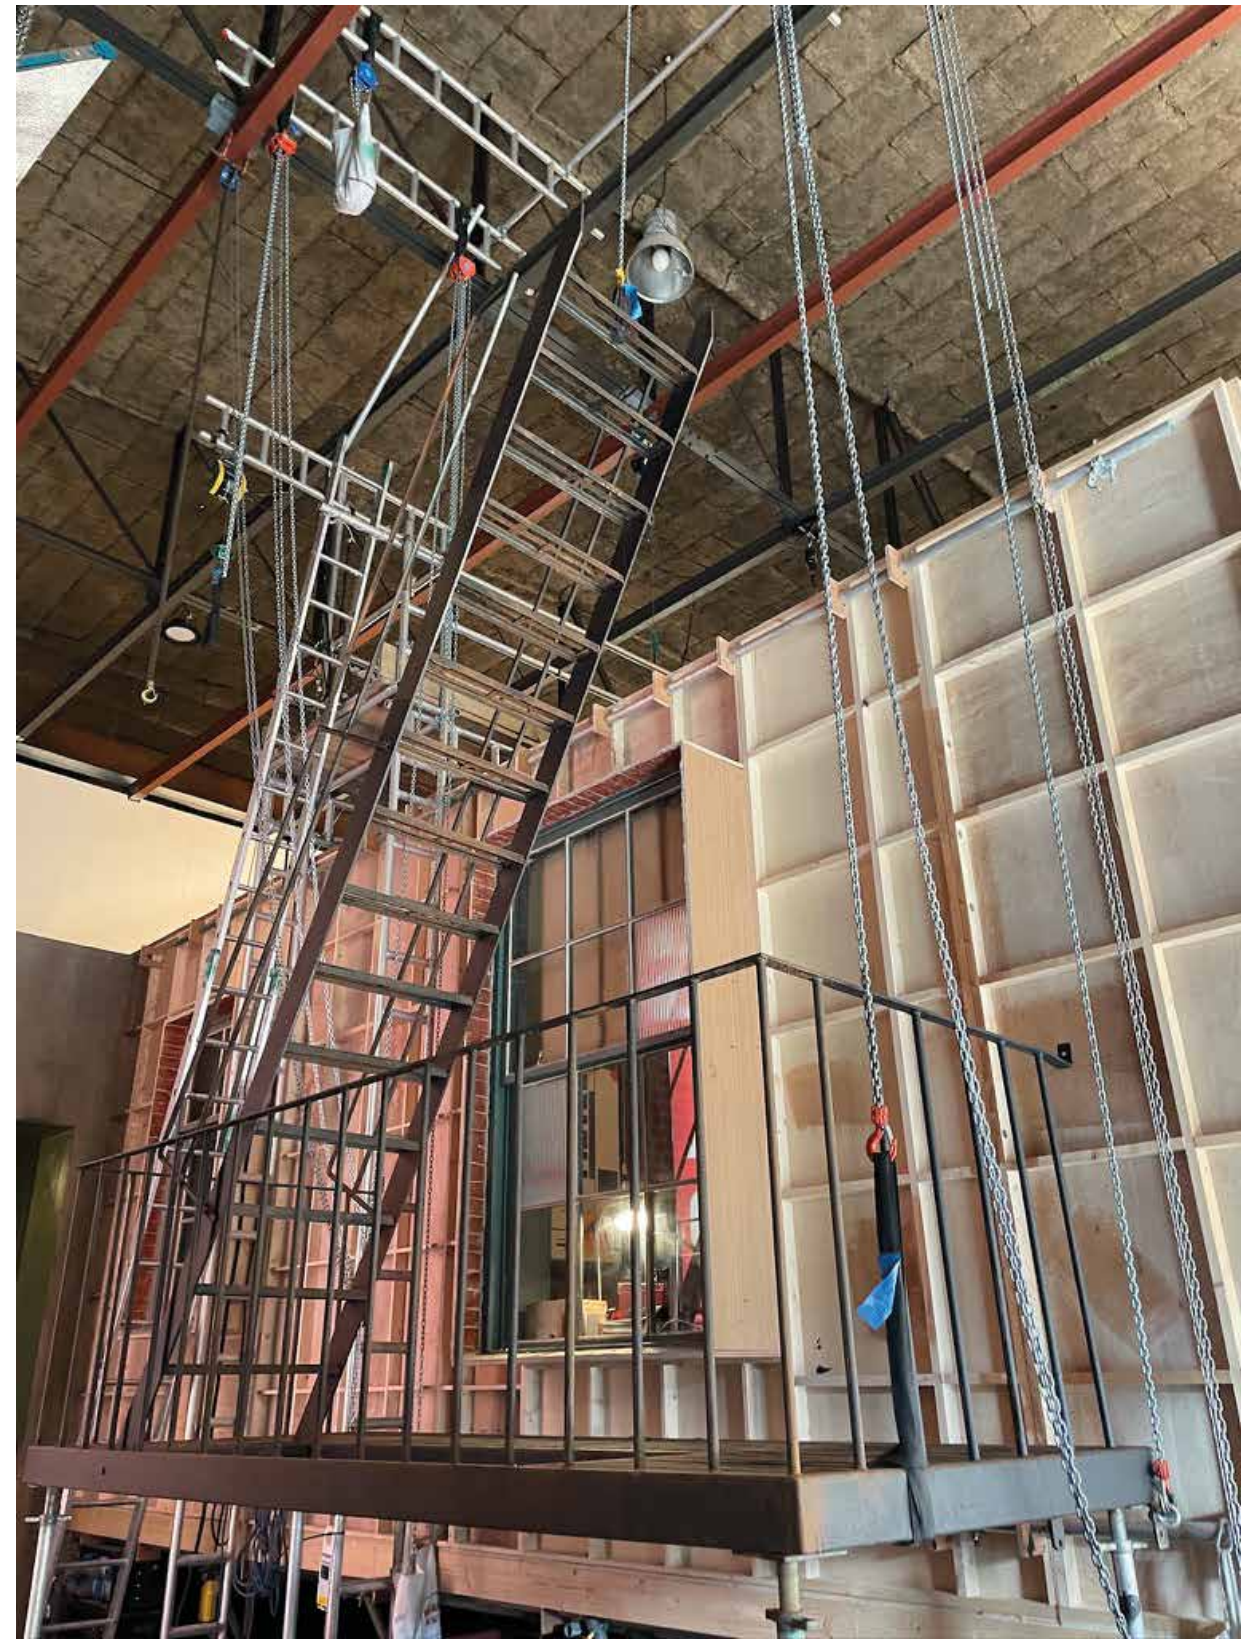





STAND TYPE 'A'  
NARROWER BASE, NO PLINTH

x6

Front Elevation - Type A  
Scale: 1" : 1'

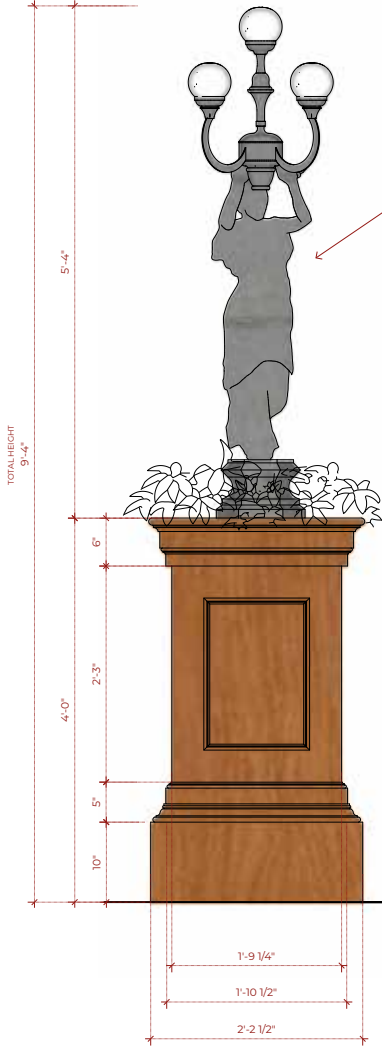


Plan - Type A  
Scale: 1" : 1'

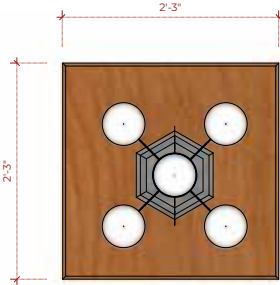


STAND TYPE 'B'  
CENTRAL PLINTH 1' 3" IN HEIGHT

x6


Front Elevation - Type B  
Scale: 1" : 1'

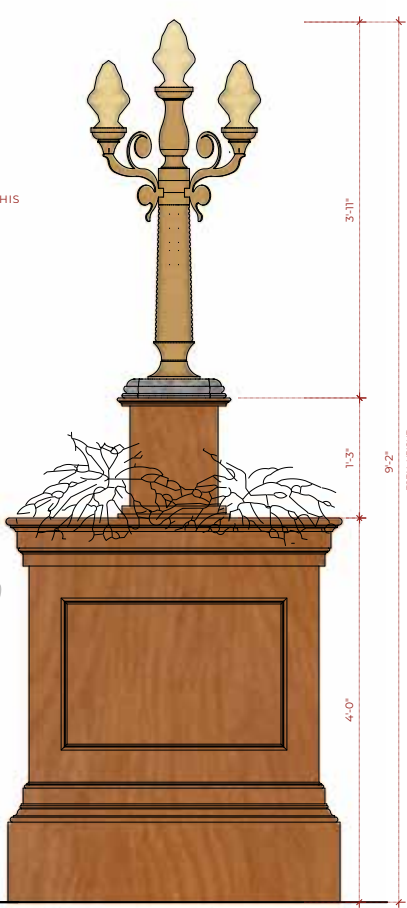


Plan - Type B  
Scale: 1" : 1'

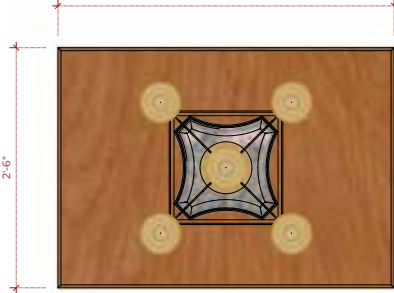

Typical Side Elevation For Type B & Type C  
Scale: 1" : 1'

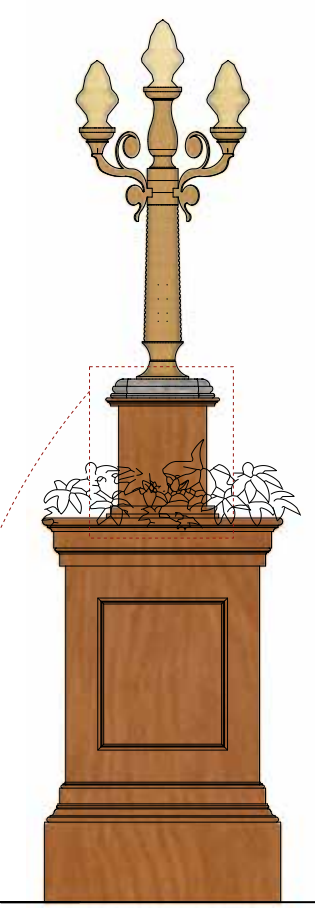


Plinth Detail - Type B  
Scale: 3" : 1'

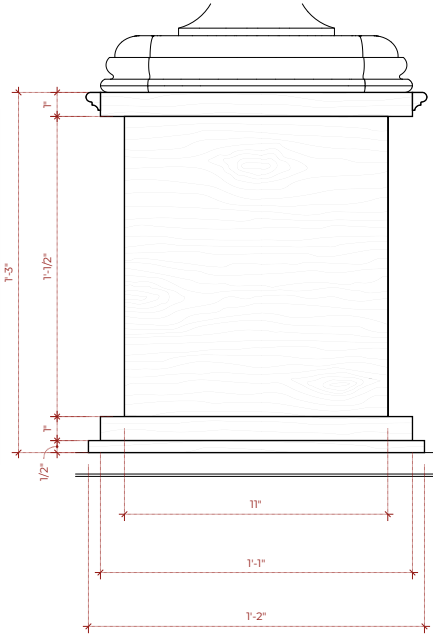


STAND TYPE 'C'  
CENTRAL PLINTH 9" IN HEIGHT

x4


Front Elevation - Type C  
Scale: 1" : 1'

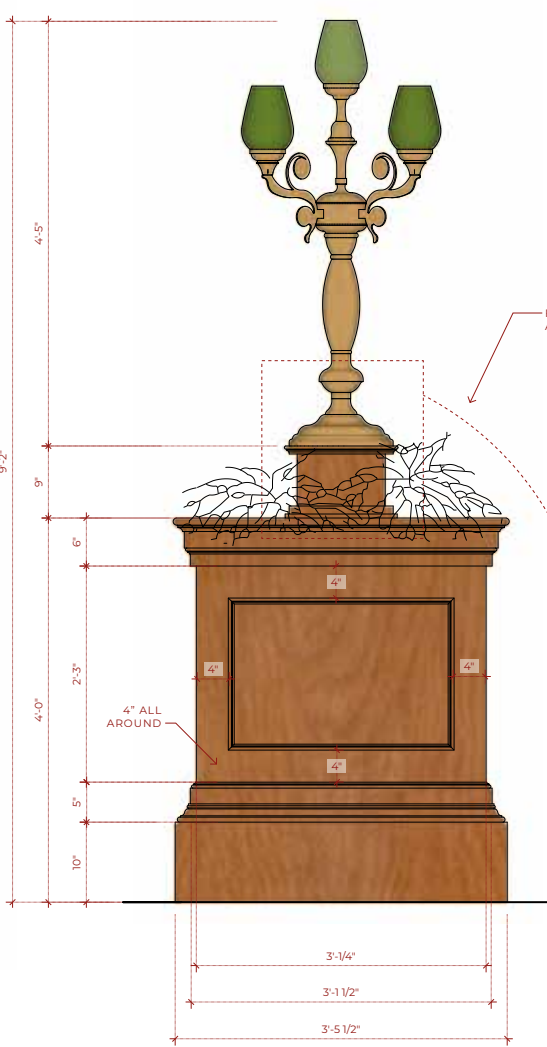



Plan - Type C  
Scale: 1" : 1'

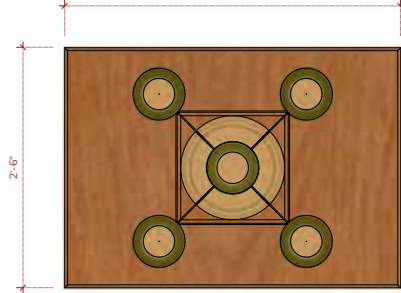

Typical Section For Type B & Type C  
Scale: 1" : 1'

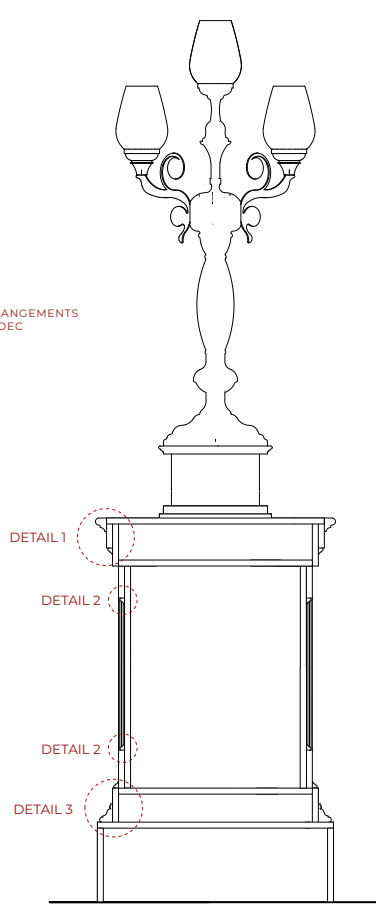

Plinth Detail - Type C  
Scale: 3" : 1'

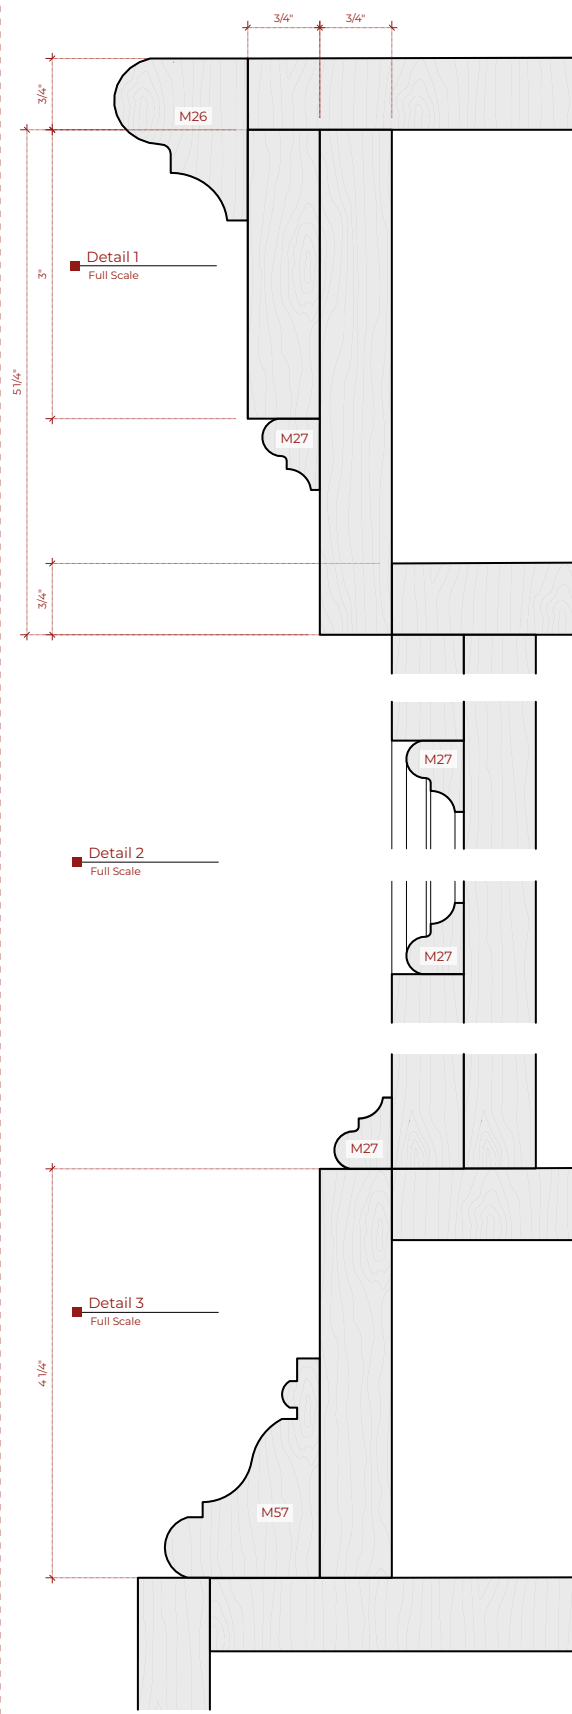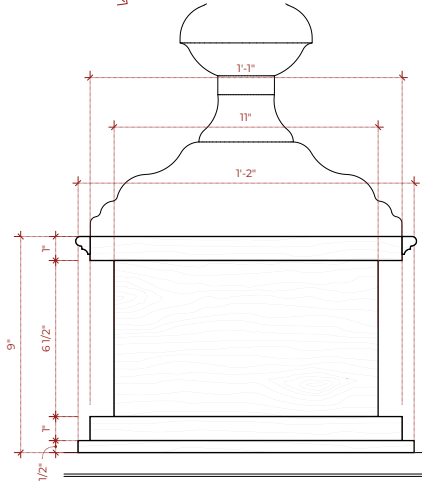

**NB CONSTRUCTION:**  
QTY x16 UNITS IN TOTAL  
TO BE CONSTRUCTED FROM PLYWOOD  
CORNERS MITRED TO CONCEAL PLY EDGE  
MOULDINGS TO BE USED AS SHOWN OR NEAREST AVAILABLE

**NB PAINTERS:**  
MAHOGANY FINISH

**NB SET DEC**  
TO PROVIDE DECORATIVE LIGHTS AS PER PROVIDED REFERENCE  
TO PROVIDE FLORAL ARRANGEMENTS AS INDICATED


ISSUED 07-10-24

| SOULM8TE    |                   |                   |  |              |  |            | DESIGNER<br>SUSIE CULLEN |                     |
|-------------|-------------------|-------------------|--|--------------|--|------------|--------------------------|---------------------|
| SET         |                   | HISTORIC BUILDING |  |              |  |            | DWG No.                  | 055                 |
| DETAILS     |                   | DECORATIVE STANDS |  |              |  |            | SET No.                  | 136                 |
|             |                   |                   |  |              |  |            | SCALE                    | 1" : 1', 3" : 1, FS |
| DRAWN BY    | DW                | PRODUCER          |  | DECORATOR    |  | CON. MNGR  | CAMERA                   | VFX                 |
| APPROVED    | SC                | DIRECTOR          |  | BUYER        |  | CARPENTERS | GAFFER                   | SFX                 |
| DATE DRAWN  | 02.10.2024        | PRODUCTION        |  | PROPS        |  | PLASTERERS | METAL                    | ART                 |
| DATE ISSUED | 07.10.2024        | LOCATIONS         |  | DRAPES       |  | PAINTERS   | RIGGERS                  | GFX                 |
| LOCATION    | CITY HALL, DUBLIN | MODELMAKERS       |  | CONSTRUCTION |  | MOULMAKERS | STUNTS                   | GREENS              |



Typical Section - Type A & B  
Scale: 1/4" = 1'-0"


WINDOW  
TYPE 'A'  
LIGHTWELL WINDOWS  
4x

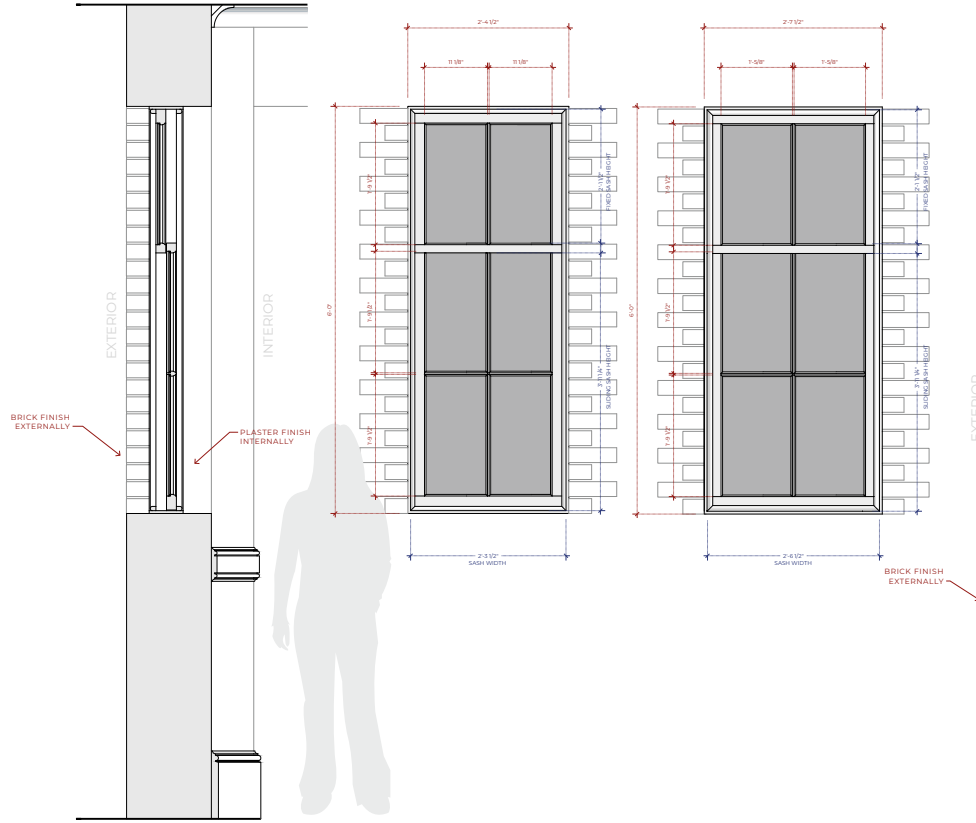

WINDOW  
TYPE 'B'  
END OF HALLWAY  
1x


Typical Section - Type C  
Scale: 1/4" = 1'-0"

WINDOW  
TYPE 'C'  
STORE ROOM  
1x

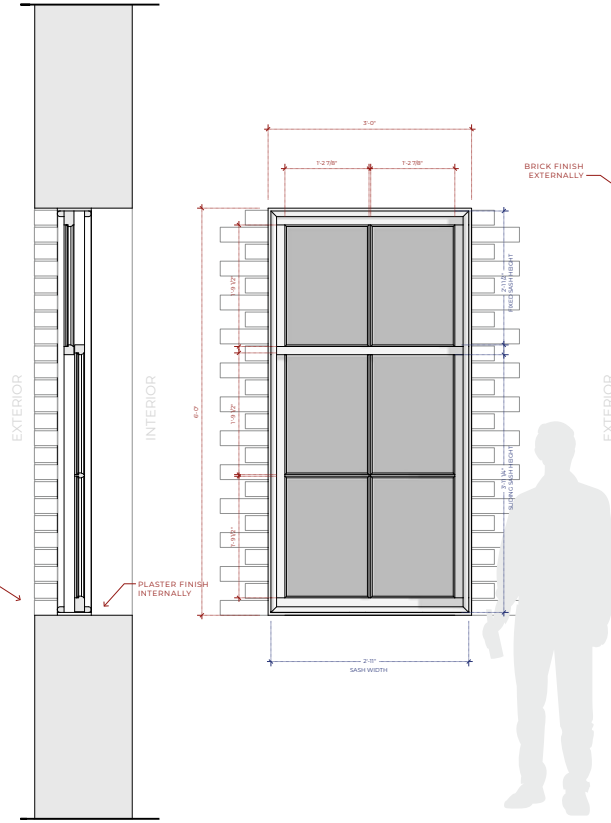


Typical Section - Type D  
Scale: 1/4" = 1'-0"


WINDOW  
TYPE 'D'  
BED ROOM  
1x

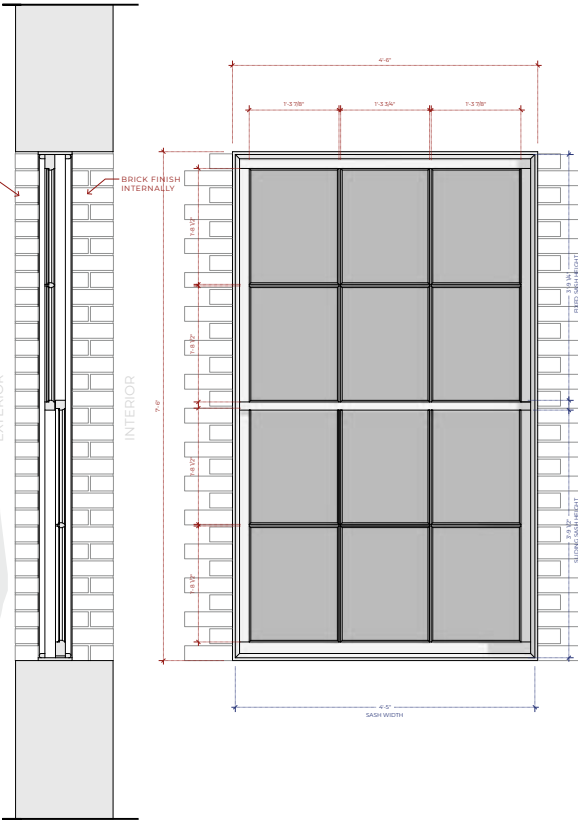


Typical Detail - Section  
Scale: Full Scale

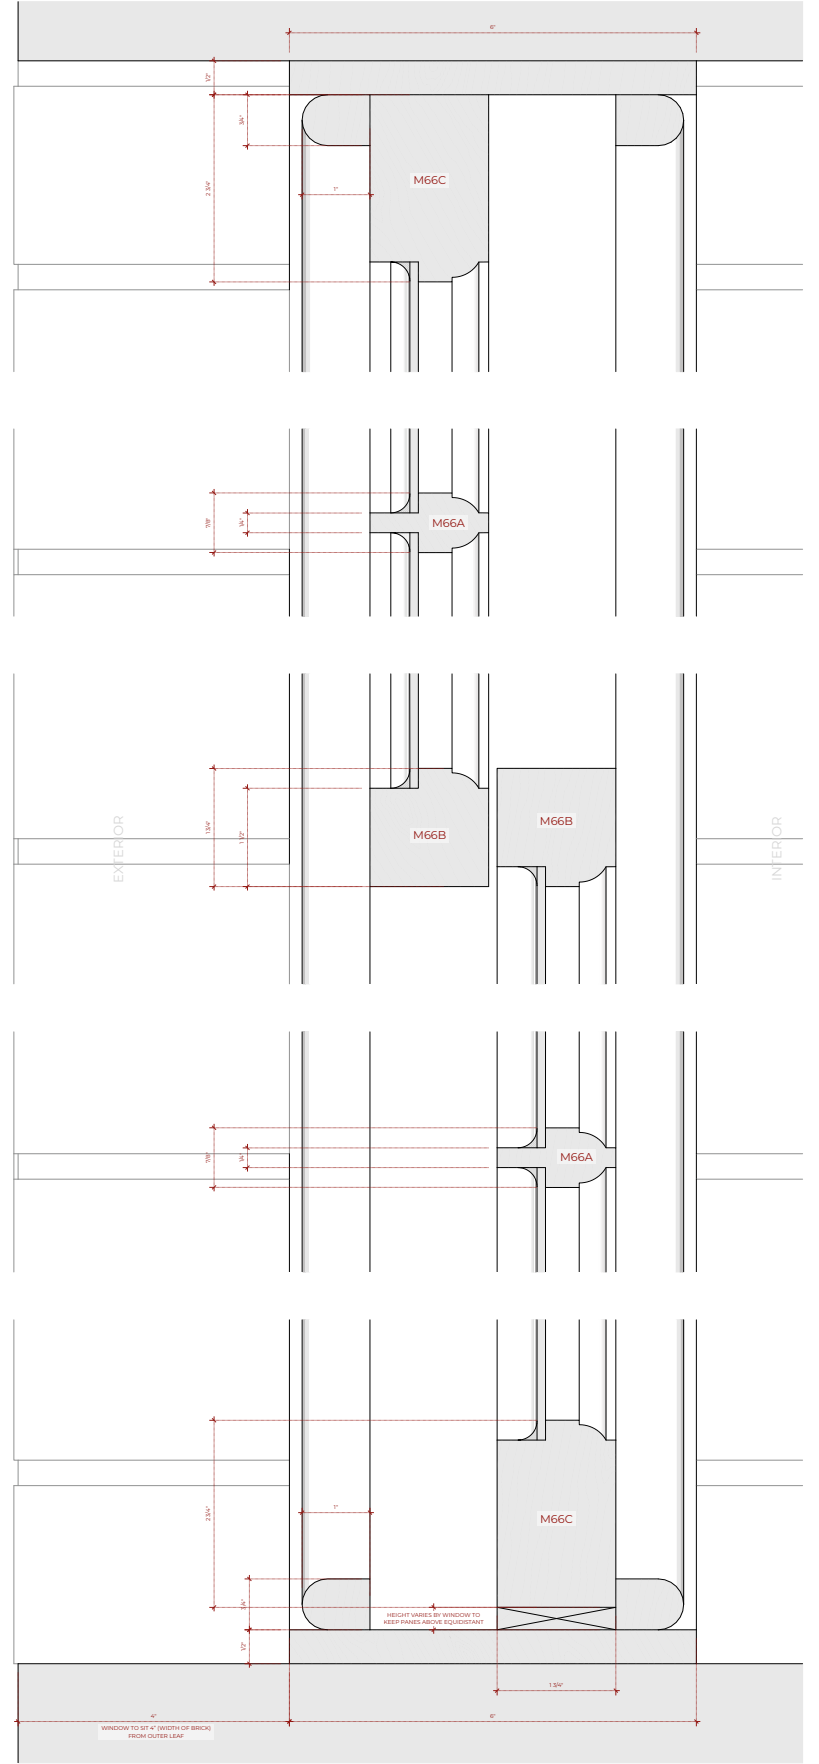

Key Plan  
Scale: 1/8" = 1'-0"

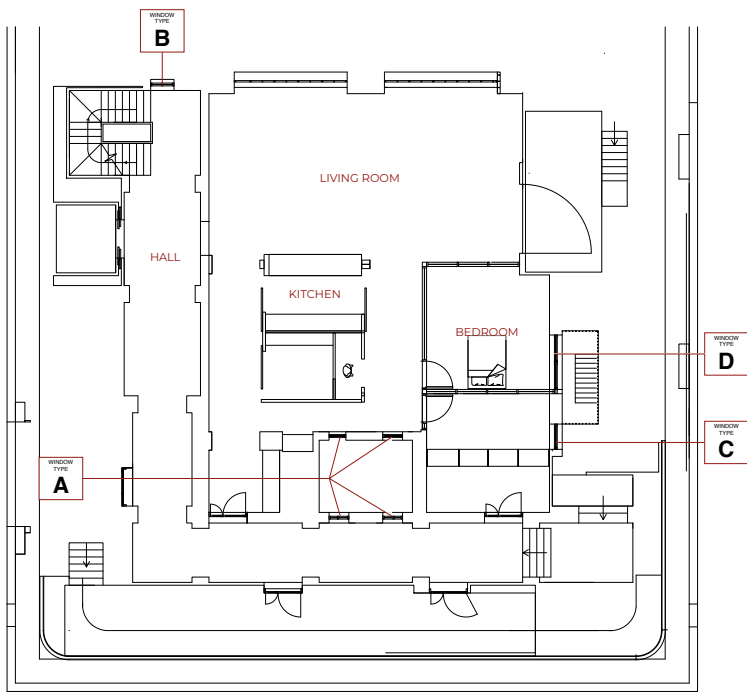

Typical Detail - Plan  
Scale: Full Scale

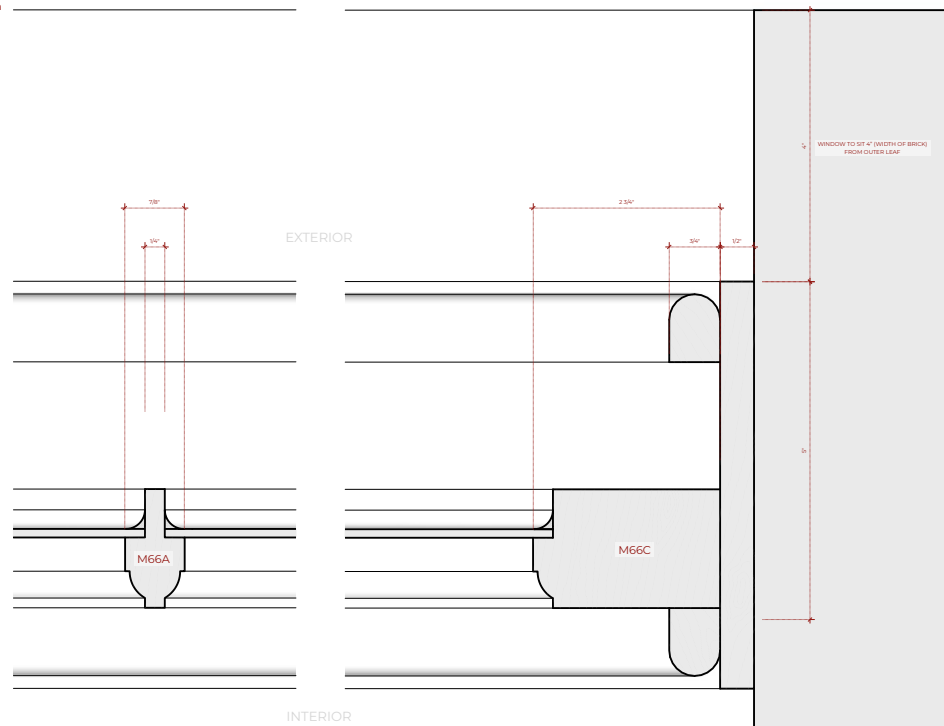

GLASS PANE SCHEDULE

| TYPE             | DIMS (W x H)          | QUANTITY PER WINDOW | TOTAL QUANTITY |
|------------------|-----------------------|---------------------|----------------|
| A                | 11'1/8" x 1'-9 1/2"   | x6                  | x24            |
| B                | 1'-0 5/8" x 1'-9 1/2" | x6                  | x6             |
| C                | 1'-2 7/8" x 1'-9 1/2" | x6                  | x6             |
| D (SIDE PANES)   | 1'-3 7/8" x 1'-8 1/2" | x8                  | x8             |
| D (MIDDLE PANES) | 1'-3 3/4" x 1'-8 1/2" | x4                  | x4             |



**NB CONSTRUCTION:**  
MANSFIELD MOULDING M66 TO BE USED THROUGHOUT  
WINDOWS TO BE 1x WIDTH OF BRICK FROM OUTER LEAF 1x 4" AS INDICATED  
WINDOWS **A, B & C** HAVE BRICK FINISH ON EXTERIOR AND PLASTER FINISH INTERIOR  
WINDOW **D** HAS BRICK FINISH ON EXTERIOR AND INTERIOR SURFACE RETURNING TO WINDOW

**NB SET DEC:**  
WINDOW FURNITURE TO BE PURCHASED AS PER REFERENCES TO FOLLOW

ISSUED 04.09.2024

| SOULM8TE          |            |              |            |              |         | DESIGNER<br>SUSIE CULLEN |              |
|-------------------|------------|--------------|------------|--------------|---------|--------------------------|--------------|
| DAVID'S APARTMENT |            |              |            |              |         | DWG No.                  | 022          |
| SASH WINDOWS      |            |              |            |              |         | SET No.                  | 111          |
| SCALE             |            |              |            |              |         | 1" = 1'-0"               | 1/8" = 1'-0" |
| DRAWN BY          | DW         | PRODUCER     | DECORATOR  | CON. MGR     | CAMERA  | VFX                      |              |
| APPROVED          | SC         | DIRECTOR     | BUYER      | CARPENTERS   | Gaffer  | SFX                      |              |
| DATE DRAWN        | 19.08.2024 | PRODUCTION   | PROPS      | PLASTERERS   | METAL   | ART                      |              |
| DATE REBUILT      | 04.09.2024 | LOCATIONS    | DRAPE      | PAINTERS     | RIGGERS | GFX                      |              |
| LOCATION          | A STAGE    | CONSTRUCTION | MODULHABIT | CONSTRUCTION | STUNTS  | GREENS                   |              |



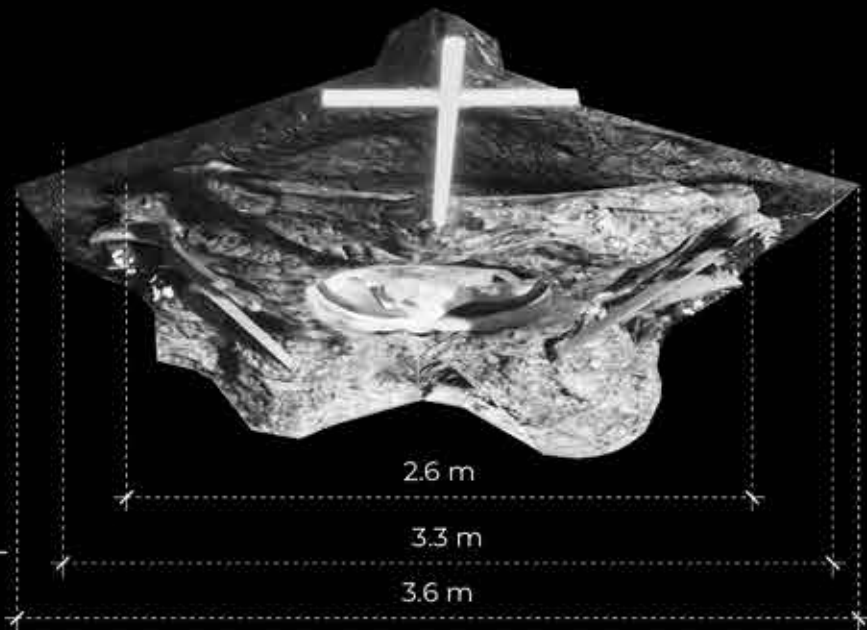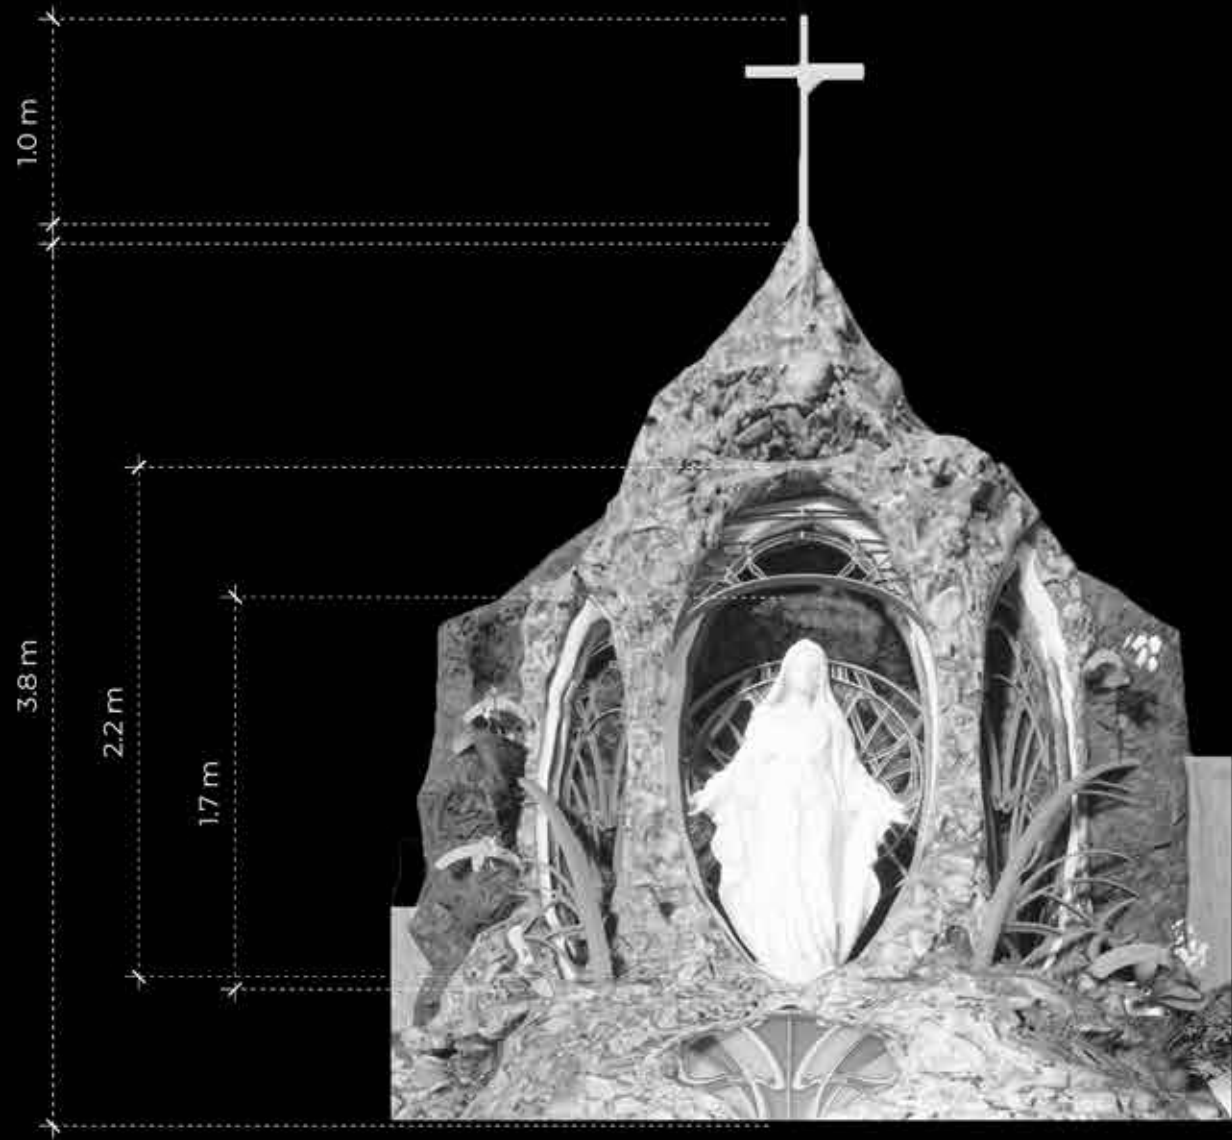

NOTE: WORK IN PROGRESS, NOT FOR CONSTRUCTION

| SET     |         | EXT CROTTO |     |          |        |  | VISITATION                                |                                   |
|---------|---------|------------|-----|----------|--------|--|-------------------------------------------|-----------------------------------|
| DETAIL  |         | CONCEPT    |     |          |        |  |                                           |                                   |
| DWG NO. | 002-A-C | SET NO.    | TBC | LOCATION | XXXXXX |  |                                           | PRODUCTION DESIGNER: LAUREN KELLY |
|         |         |            |     |          |        |  | DRAWN BY: DIARMUID WOLFE DATE: 25/11/2022 |                                   |
|         |         |            |     |          |        |  | APPROVED BY: DATE: 00.00.0000             |                                   |
|         |         |            |     |          |        |  | ISSUED: DATE: 00.00.0000                  |                                   |
|         |         |            |     |          |        |  | DRAWING SCALE: 1:24 @ A3                  |                                   |
|         |         |            |     |          |        |  | REVISION:                                 |                                   |









LIBRARY KILKENNY

This project investigated the relationship between a centre of learning and the local community it serves. It was inspired by and intended to encourage the curious joy of learning.

The process applied in the realisation of this scheme is exemplar of my method and technique, investigating the spatial sequence through quick model making and sketching, instilling the ideas of the project in the physical form.

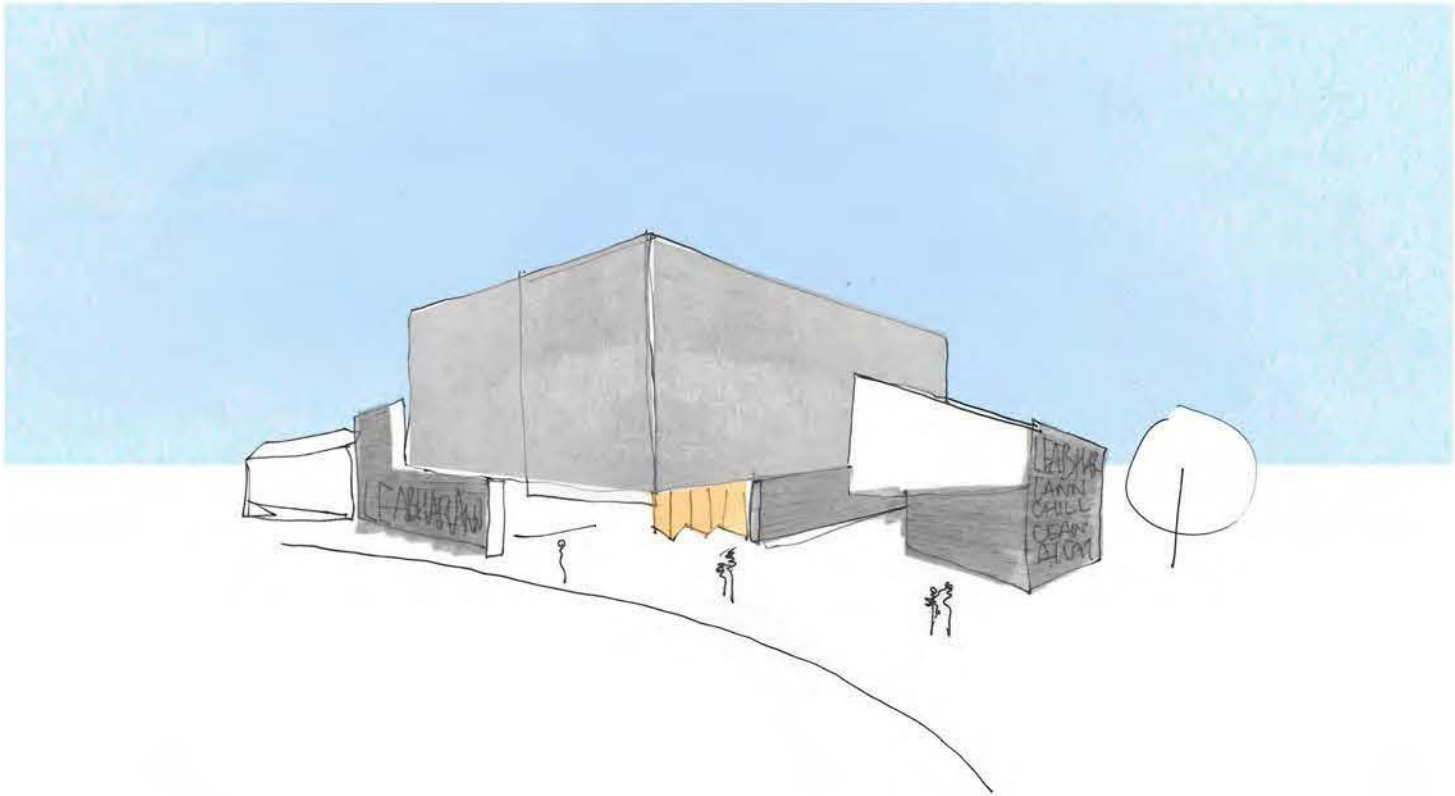



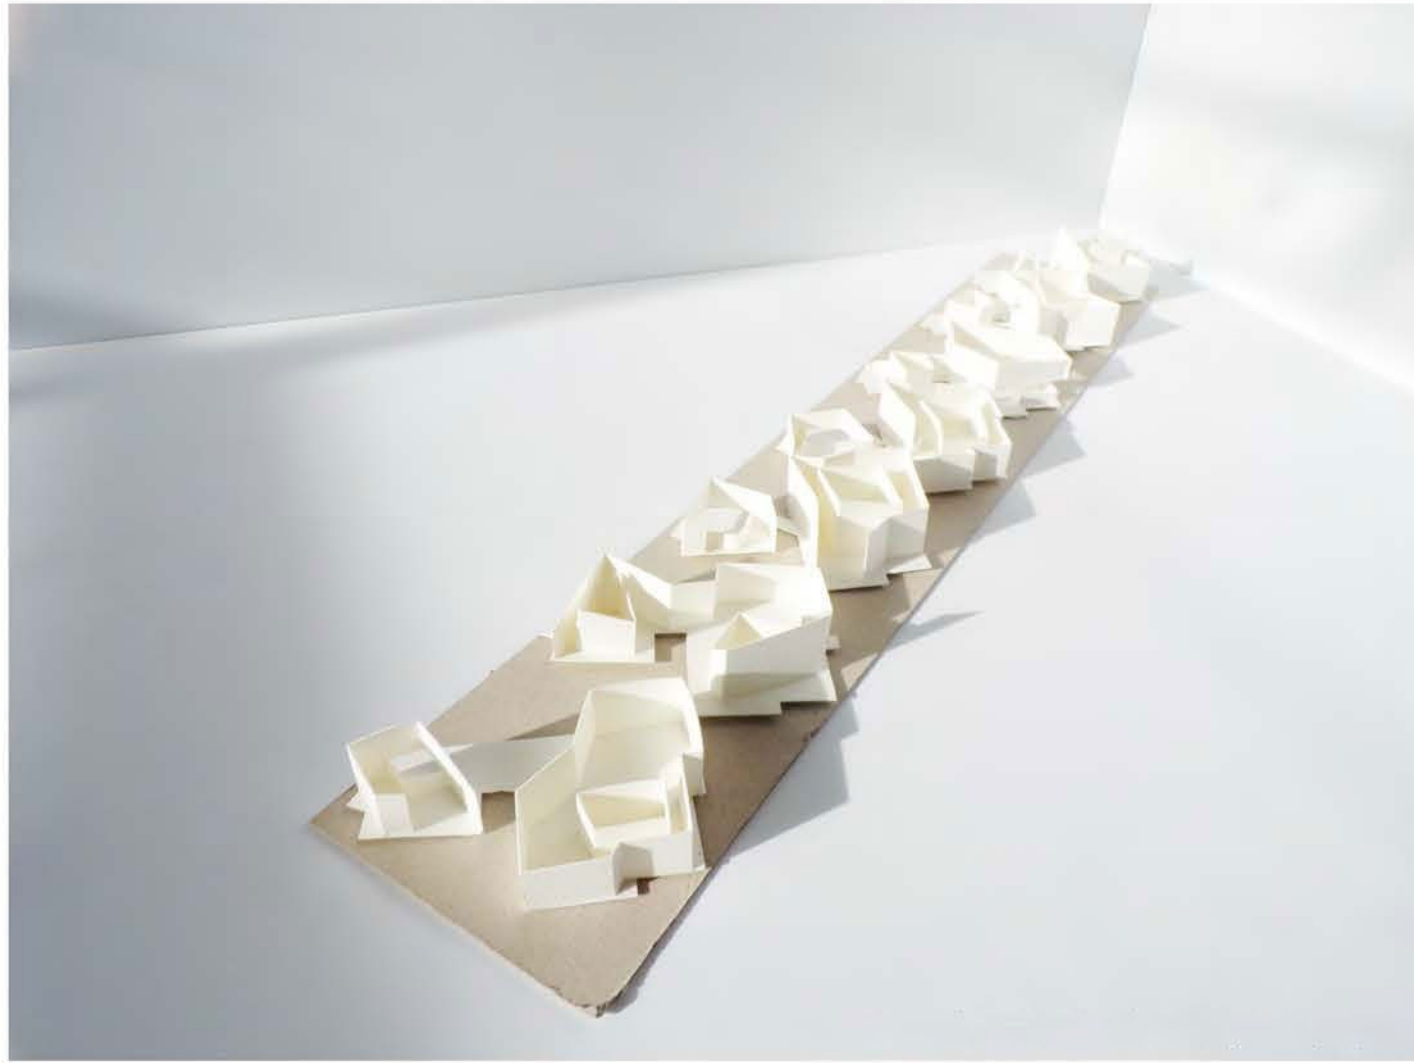


left; development of form and program through quick sketch models  
right; sketch model in context



sectional model expressing materiality and construction



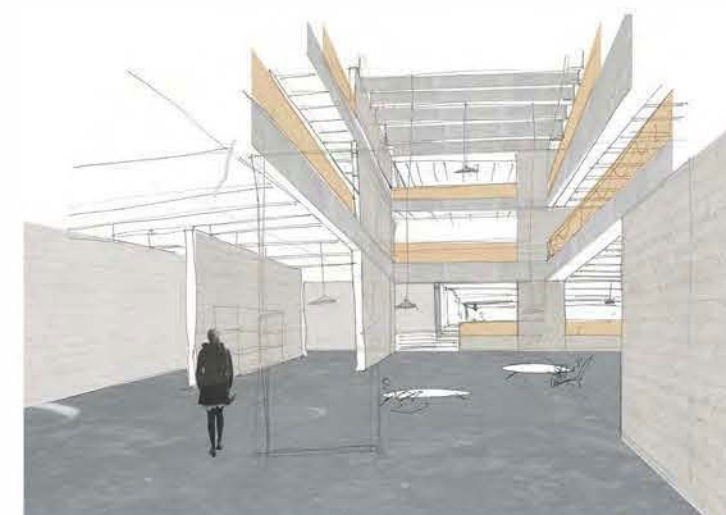

left; structural model  
right; series of sequential perspectives (hand drawn)

## URBAN VILLAGE DUBLIN DOCKLANDS



Asked to consider new forms of housing in Dublin City Centre I used this project to investigate the character of the Irish coastal village and apply it to the urban setting thereafter.

Based mostly on thoughts of active community and harmonious co-operative living the new village encourages diverse demographic co-existence.


Through model making, sketching, and perspectival drawing the scheme celebrates the warm domesticity of the Irish village, while championing the urban advantages of creating a social and sustainable infrastructure.





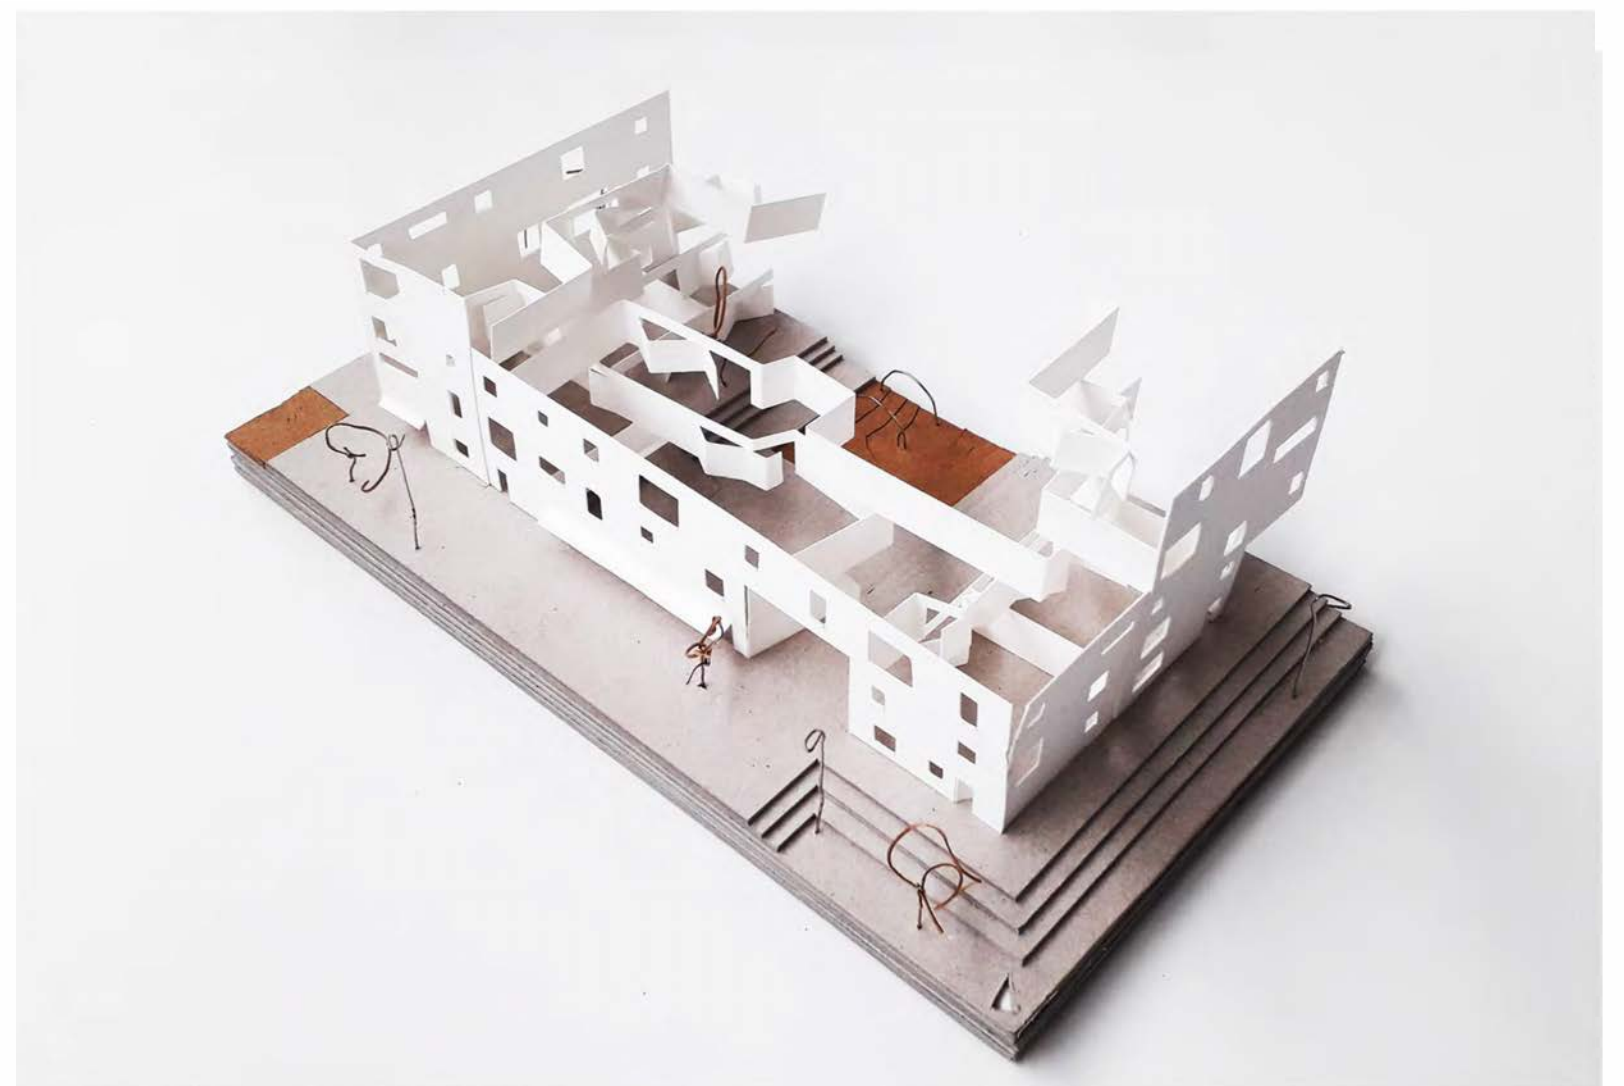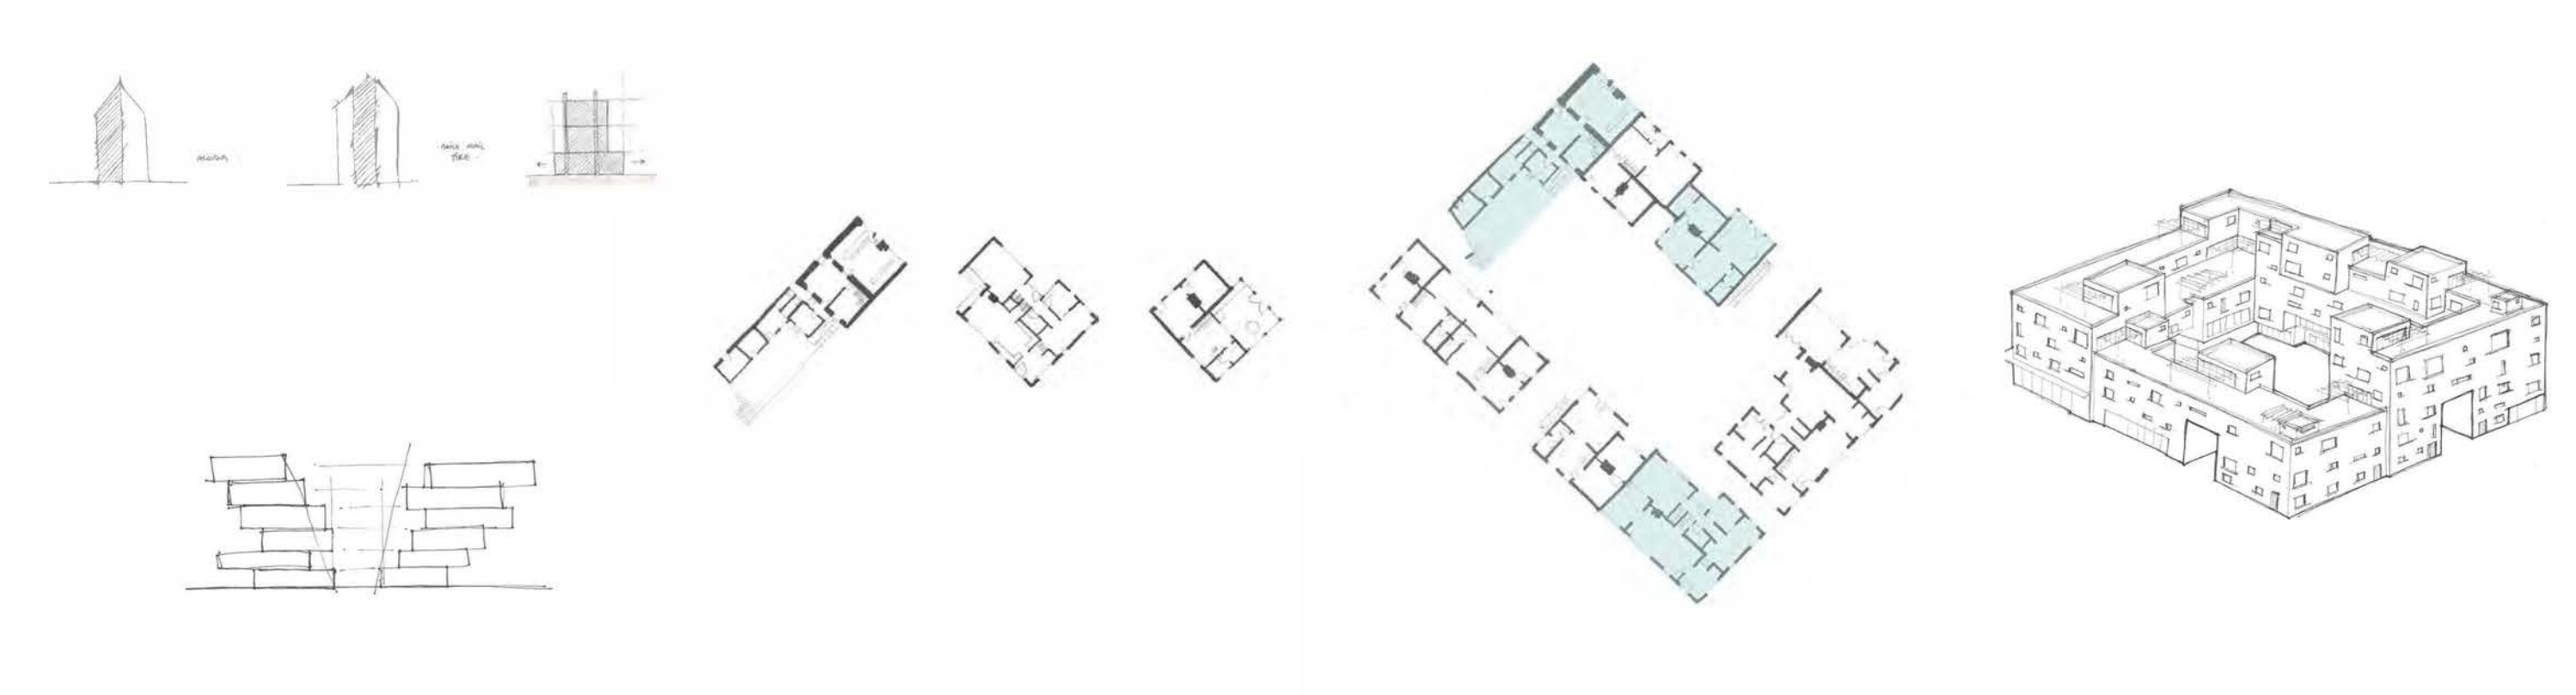

top; hand sketches and the formulation of a plan  
 right; initial sketch model, spatializing programmatic decisions

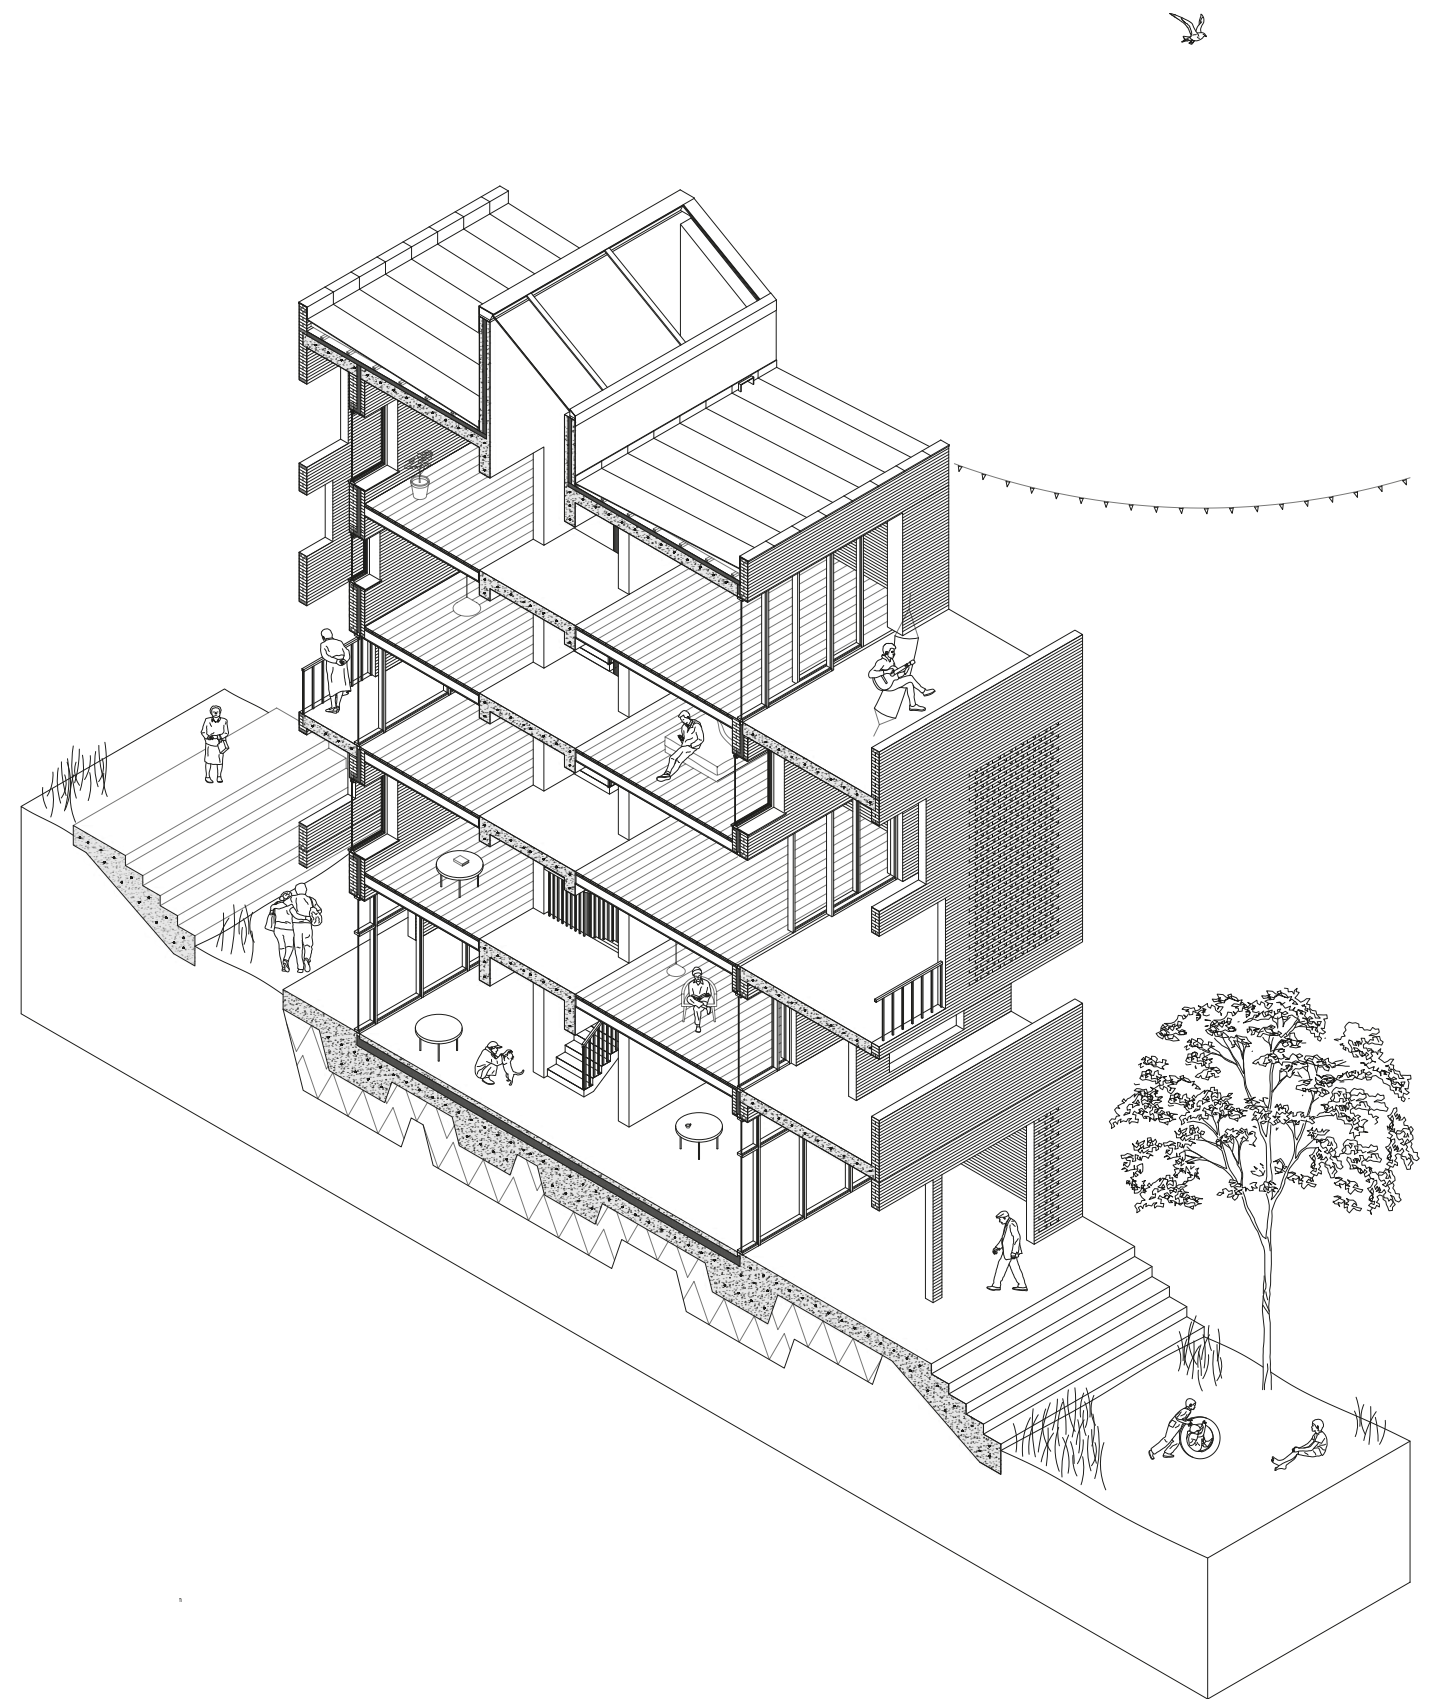

top left; perspective (hand drawn)  
 bottom left; sketch model expressing form and the interpretation of the georgian facade  
 right; sectional axonometric of housing block





left; series of sketch models exploring the housing block  
 right; model exploring environmental and contextual relationships; sea, land, civic and domestic buildings

## INTERNSHIP PARIS

I was given the opportunity to work with Shigeru Ban Architect's European base in Paris in the summer of 2019. I really enjoyed the challenge and expectation of contributing to such a prestigious practice's work.

During my time there I worked mostly in model making and sketching, the main purpose of my work being to communicate ideas between various members of the team. This communicative role meant I gained experience working on many international projects and the experience as a whole has made me a more ambitious, focused and adaptive worker.







left; model study for pavilion in Finland  
right; presentation model for art gallery extension in the south of France


## THESIS PROJECT; PUBLIC HOUSE OF CORK

This project intends to nurture understanding and sensitivity in the architectural process in learning from locale; learning from shared story, shared song and the shared spaces and places these inhabit. It is learning from the interior spatiality of places that accommodate cultural expression.



It is the public house reimagined as a sitting room for the city, a shelter for the ‘song of the city’; the unique cultural identity of its citizens, in this instance the unique cultural identity of Cork City.

In realising an architecture that spatializes these ideas the project intends to hijack existent social typologies to deliver a socially based sustainability. It is learning from ‘béaloideas’, the transmission of knowledge orally through the sharing of yarn, gossip and chat, it is learning from ‘meitheal’ in the communal effort and the promotion of collective responsibility over individualism, and it is learning from ‘seanchas’, the ‘oeuvre’ or shared imagination of the city that holds and celebrates ideas.

The architecture built from the lessons learned from locale is one of intimacy and gathering, one that encourages the sharing of identity and ideas by accommodating for the informal and colloquial transmission of knowledge through song, story, dance, tunes, poetry etc.

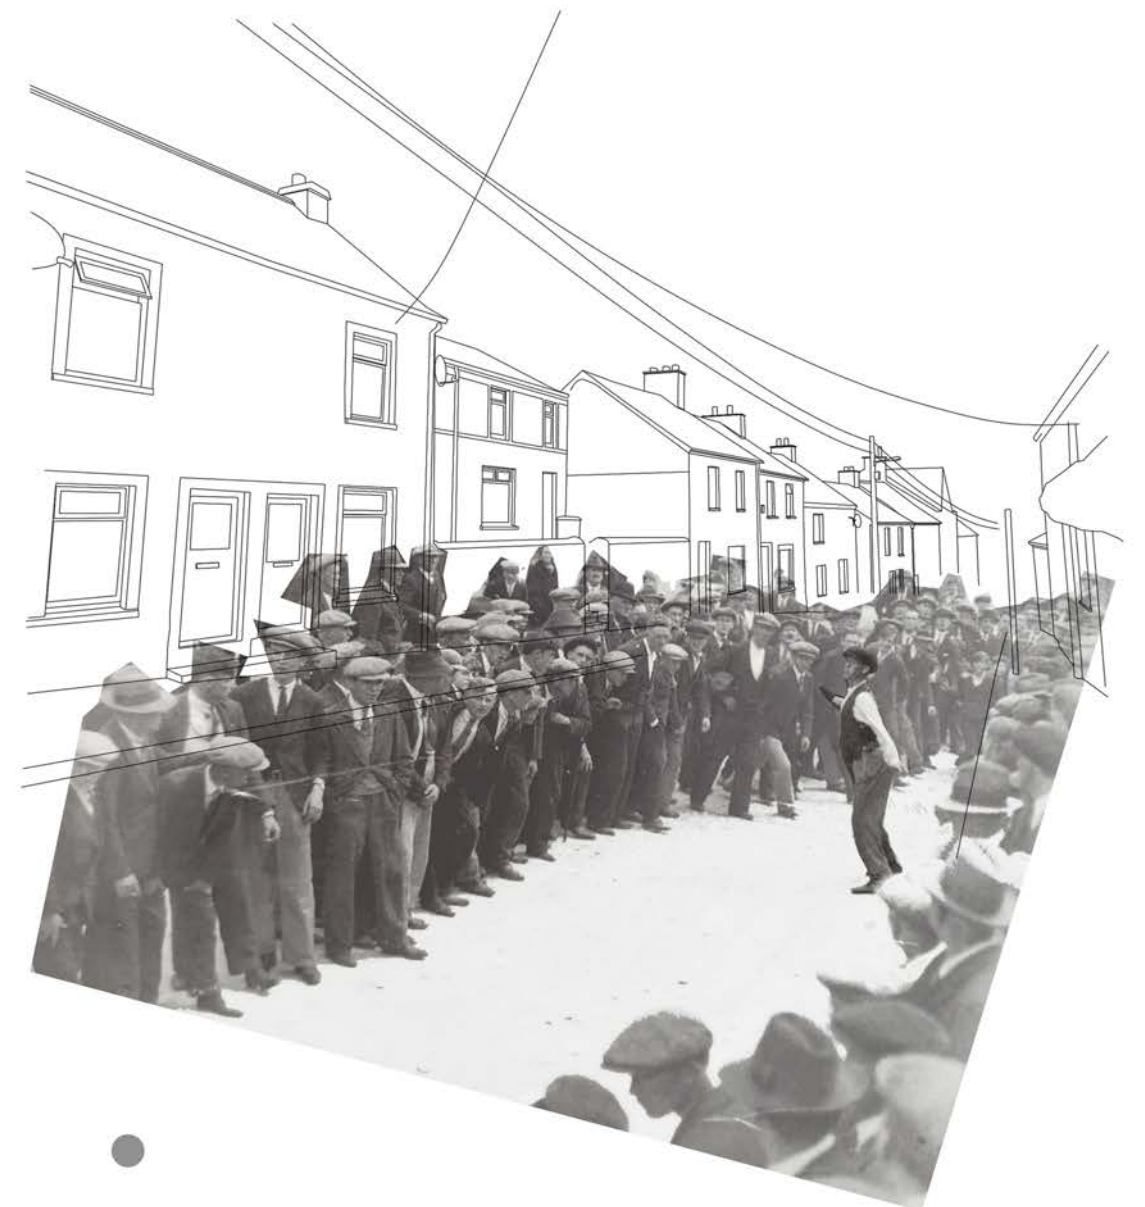



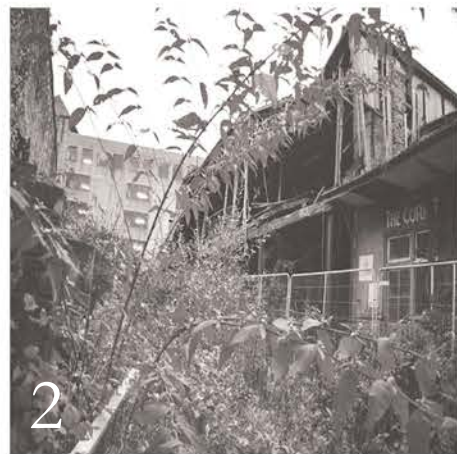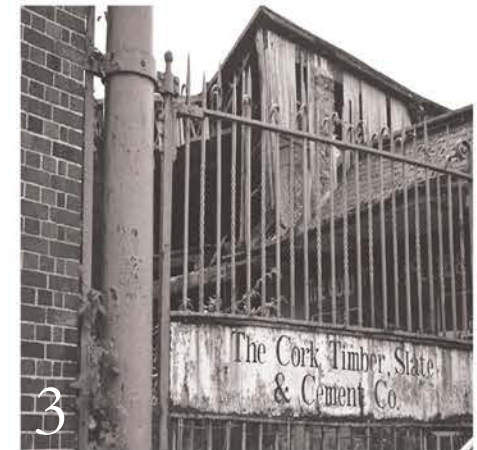

drawing studying urban grain and context







perspectival drawing showing approach from the river and kyril's quay



bird's eye looking south west

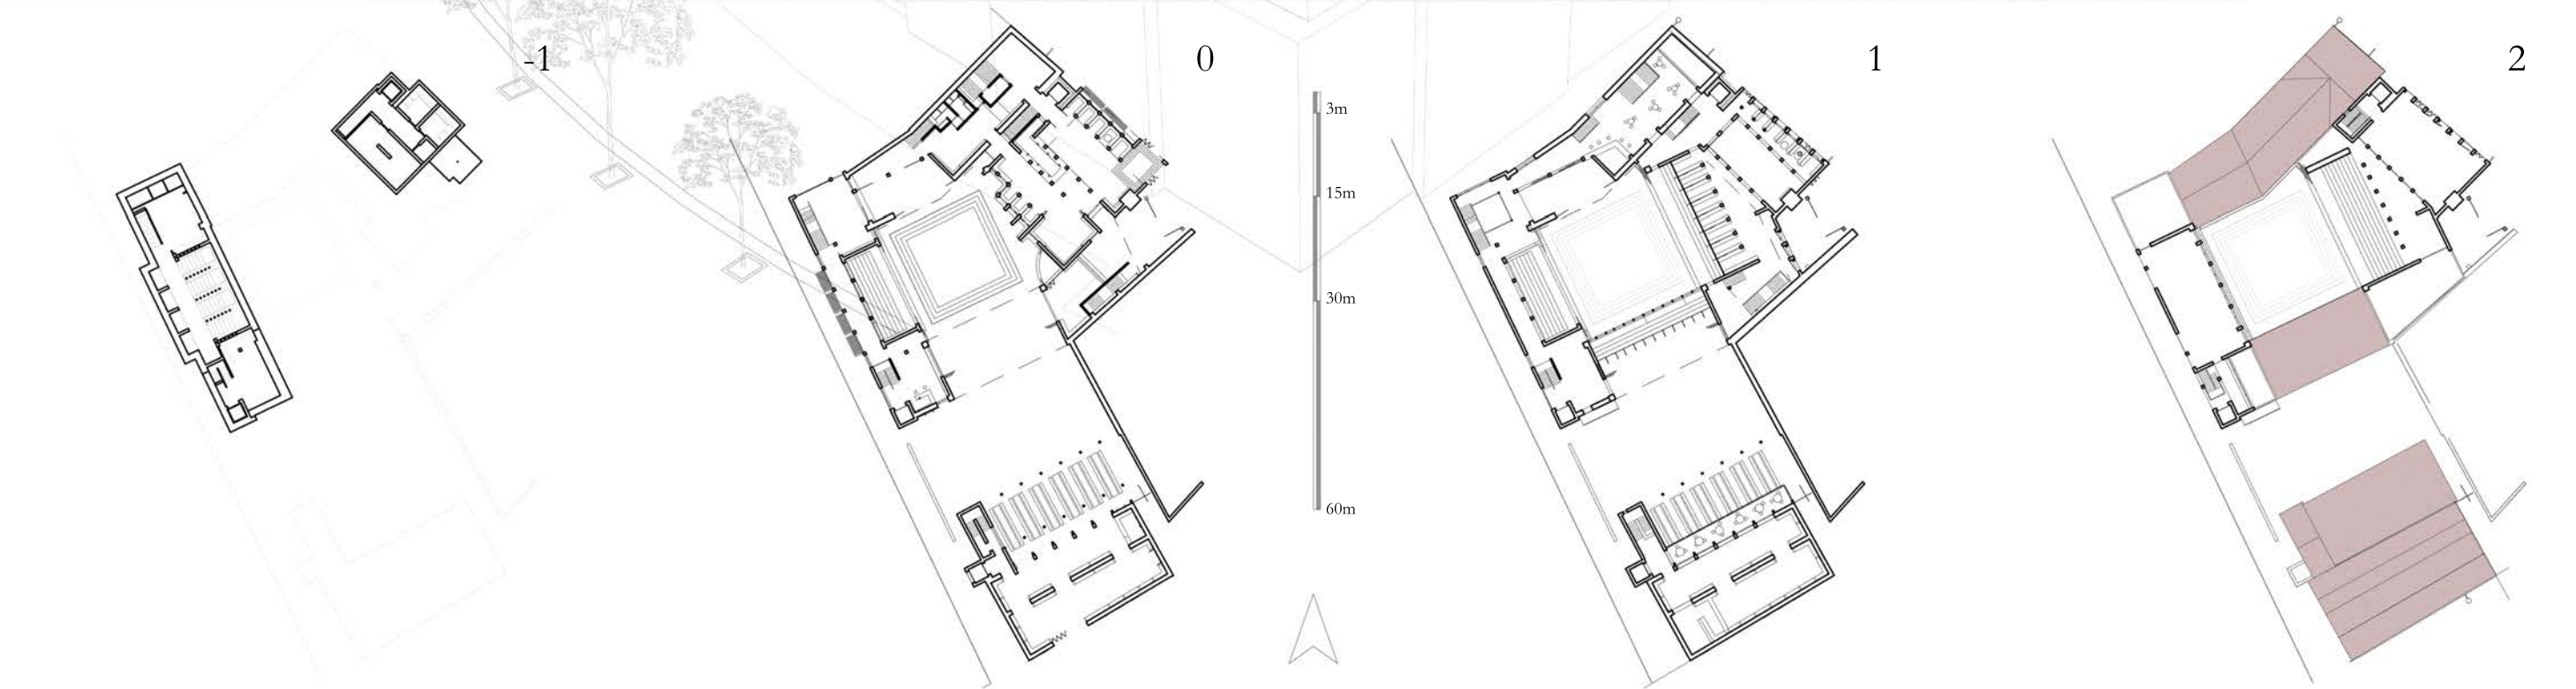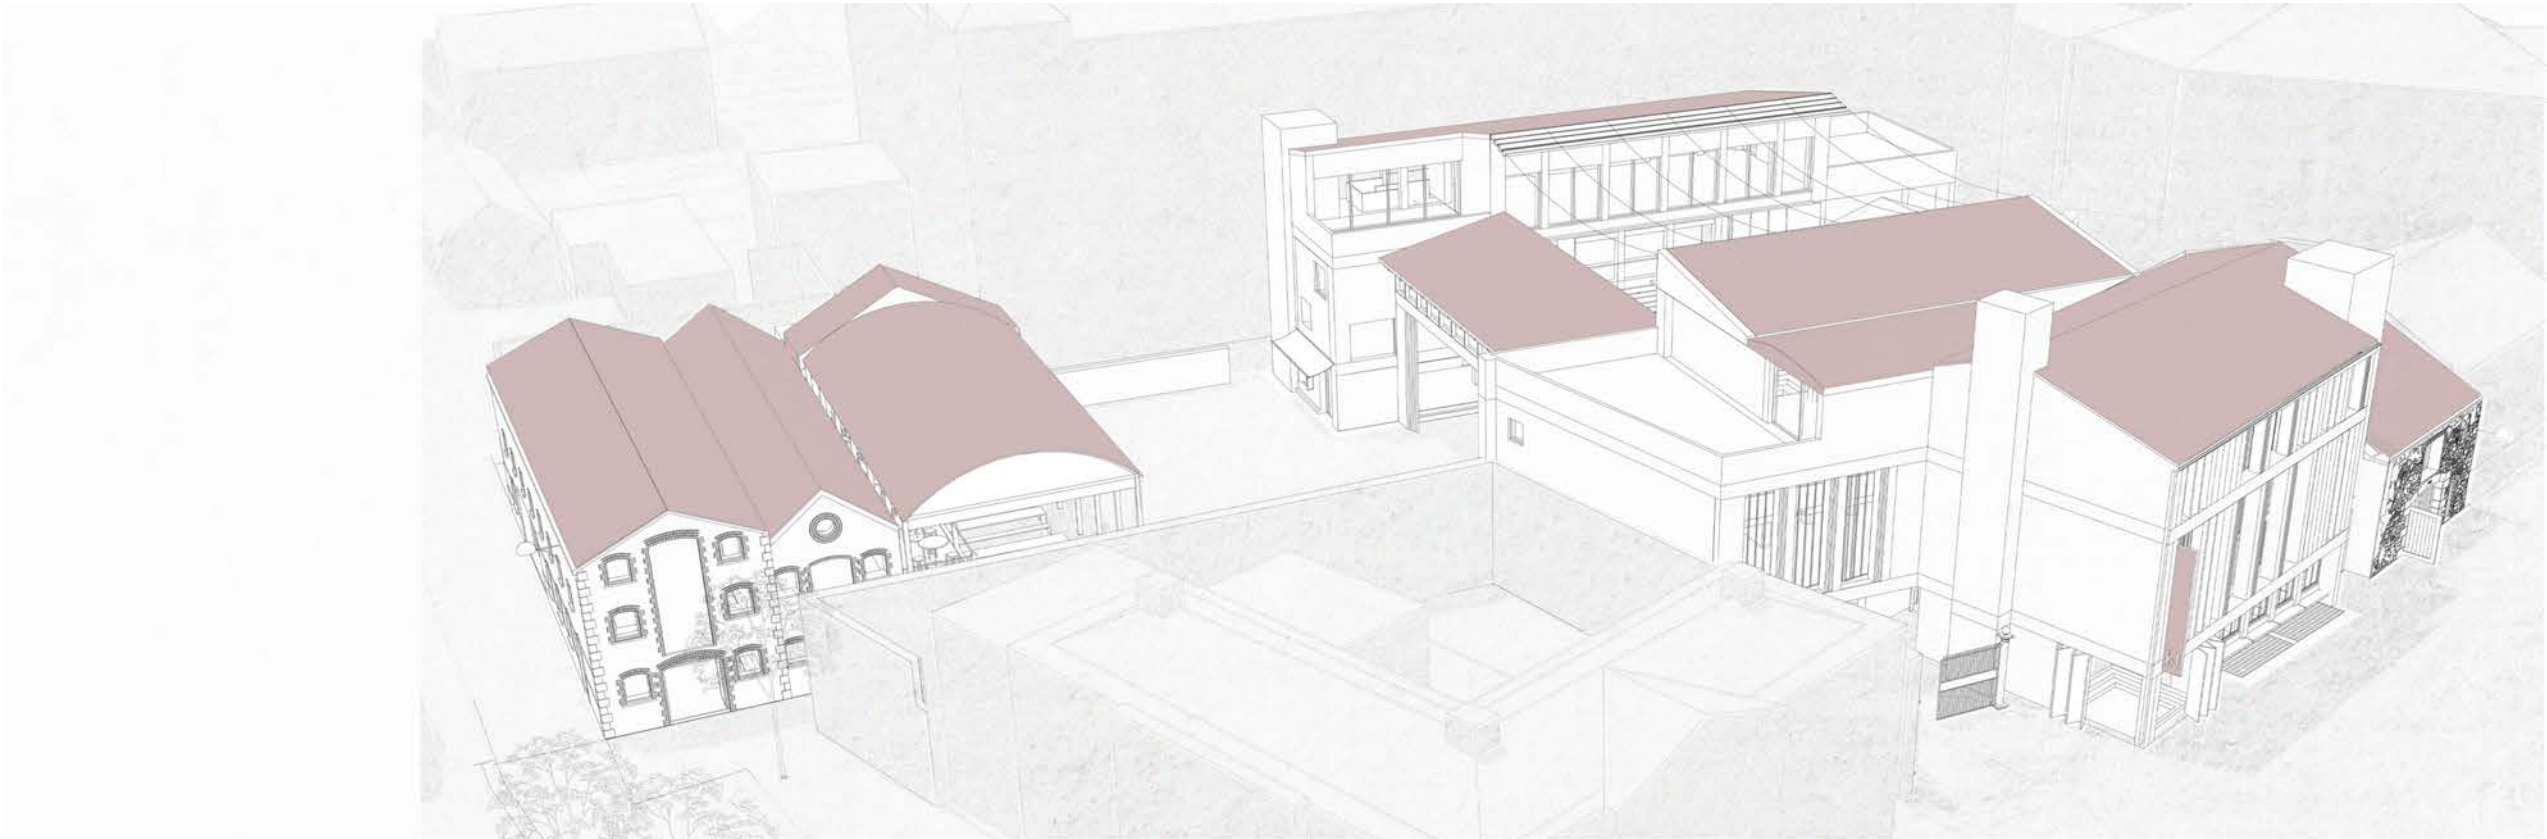

river elevation (north)



pobal  
new public space facing river


stáitse  
adaptive performance spaces

cistin  
open room facing city centre

seomra suí  
public house / bar and snugs

gairdín  
open courtyard / secret public square




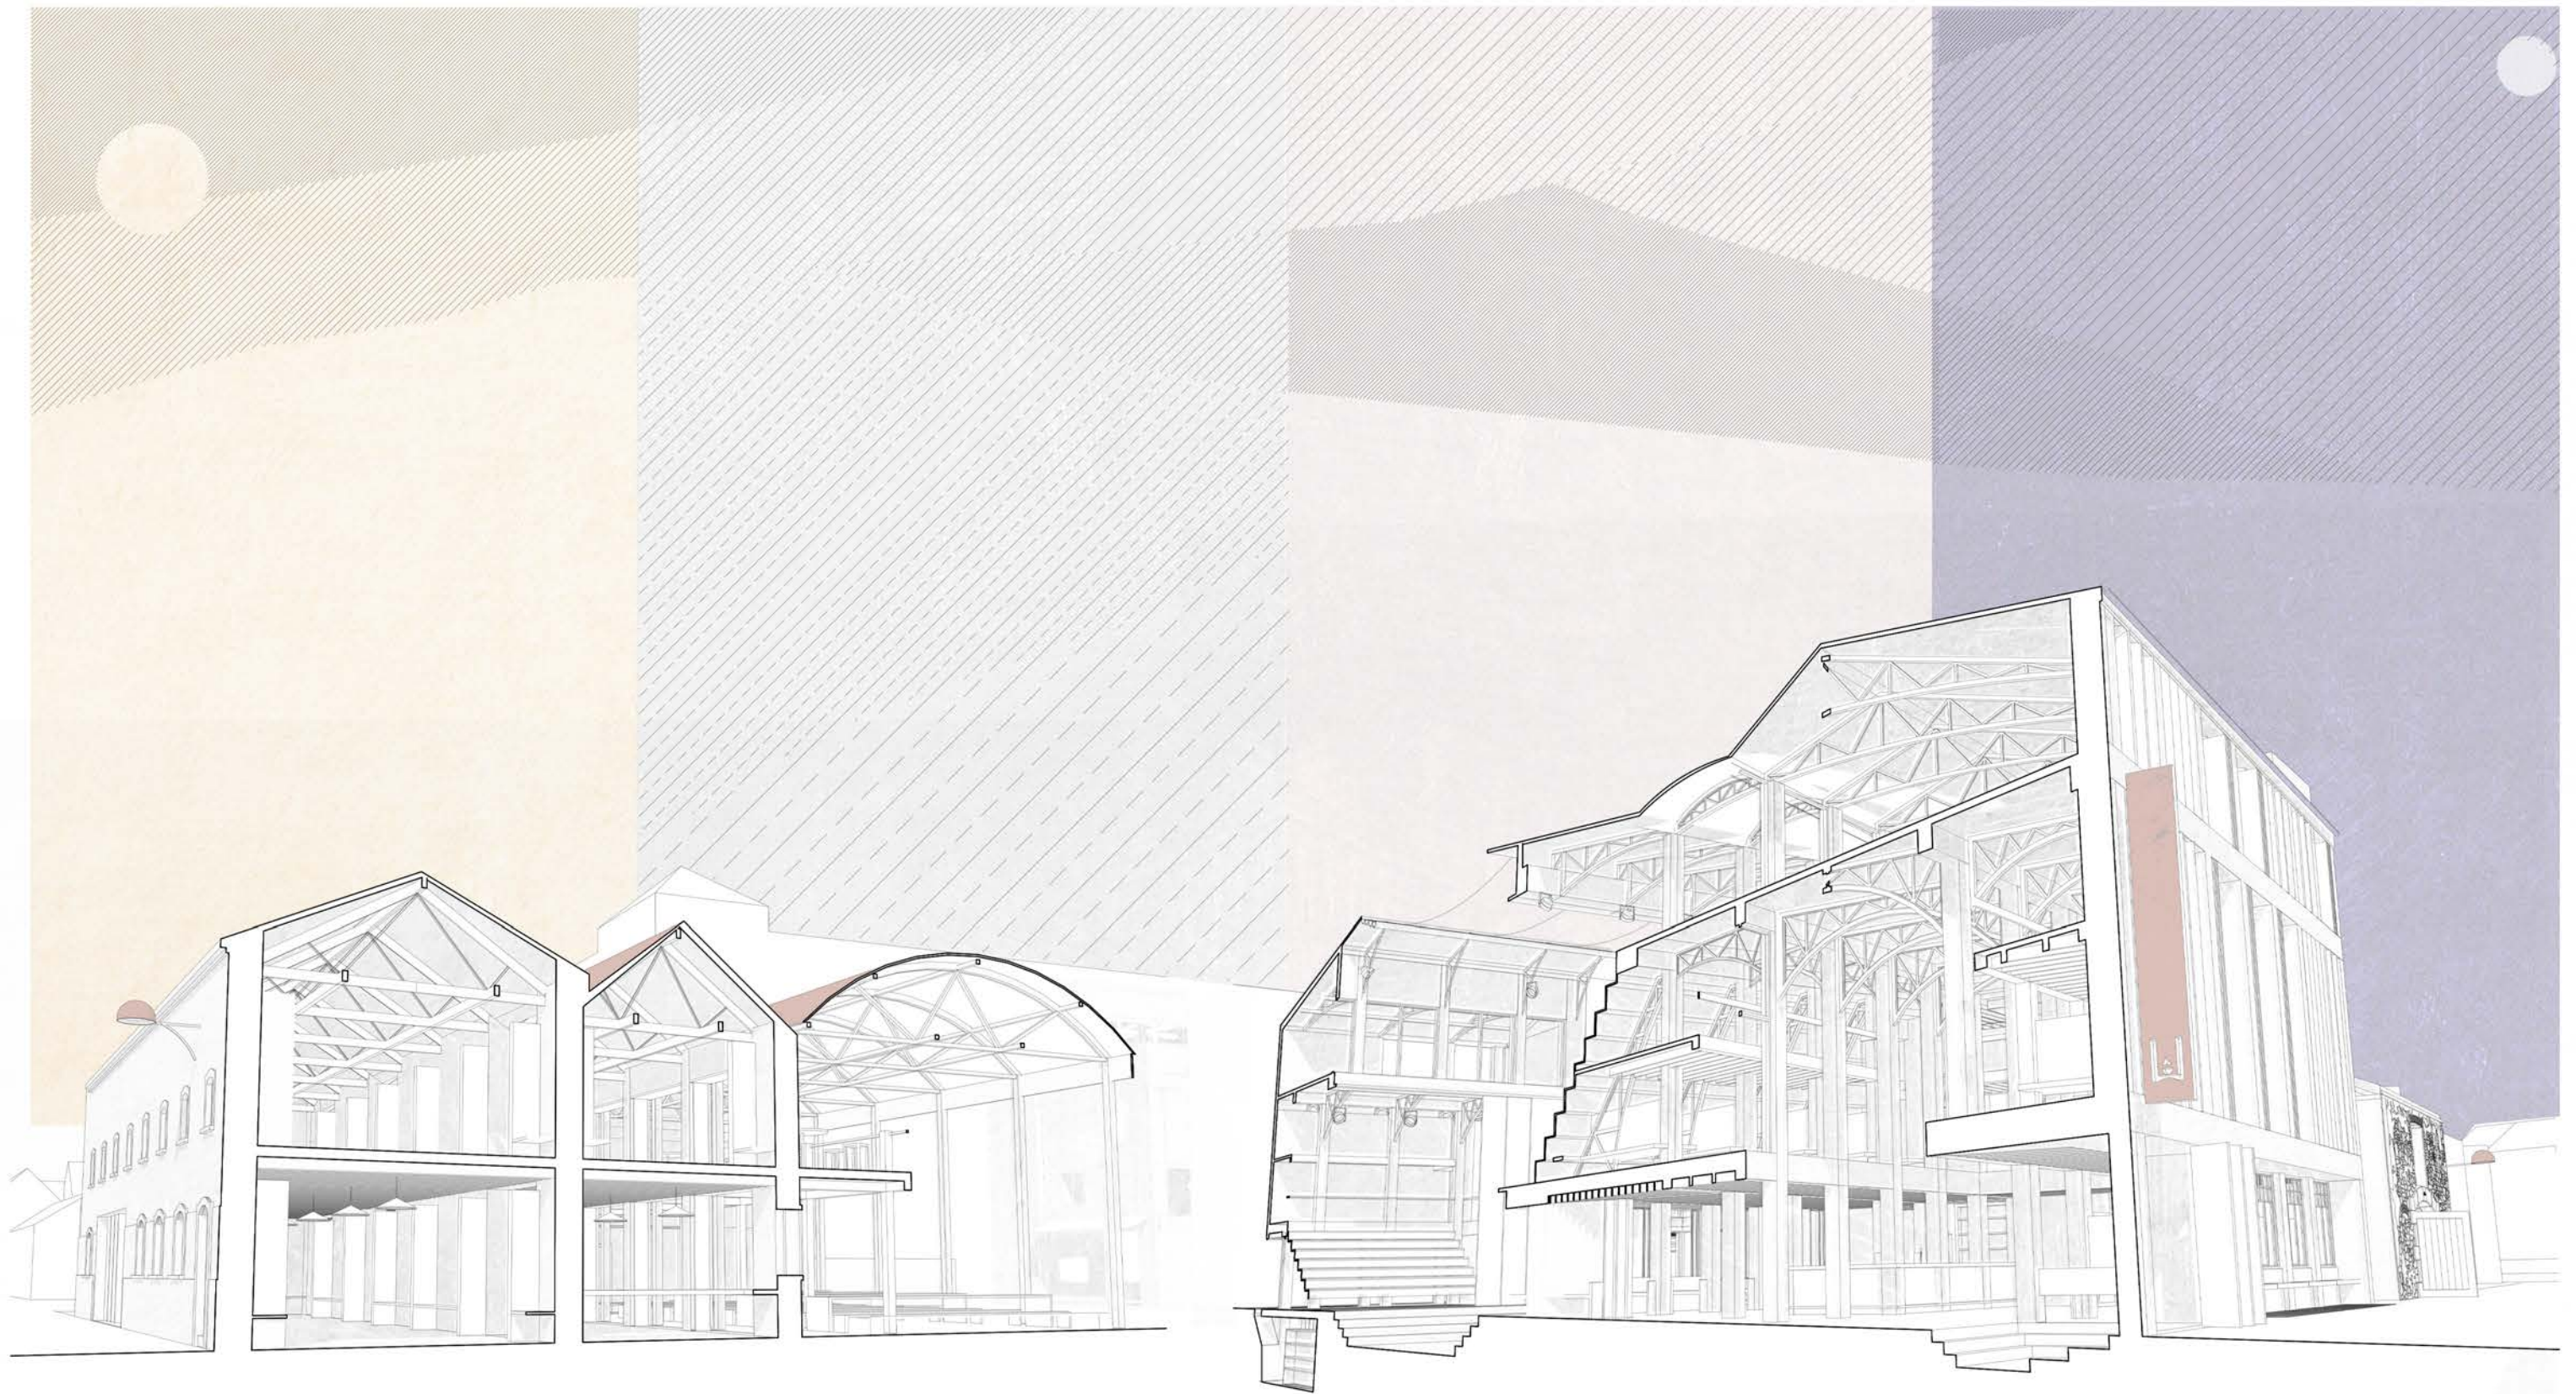


maidin




iarnóin

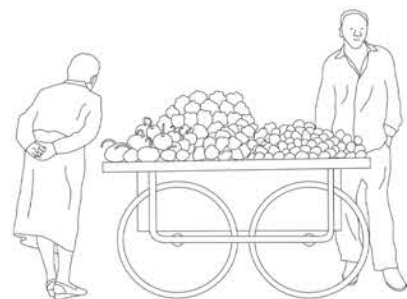


tráthnóna

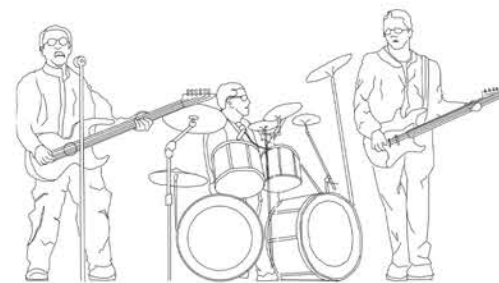

istoíche

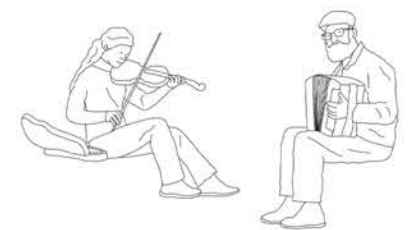





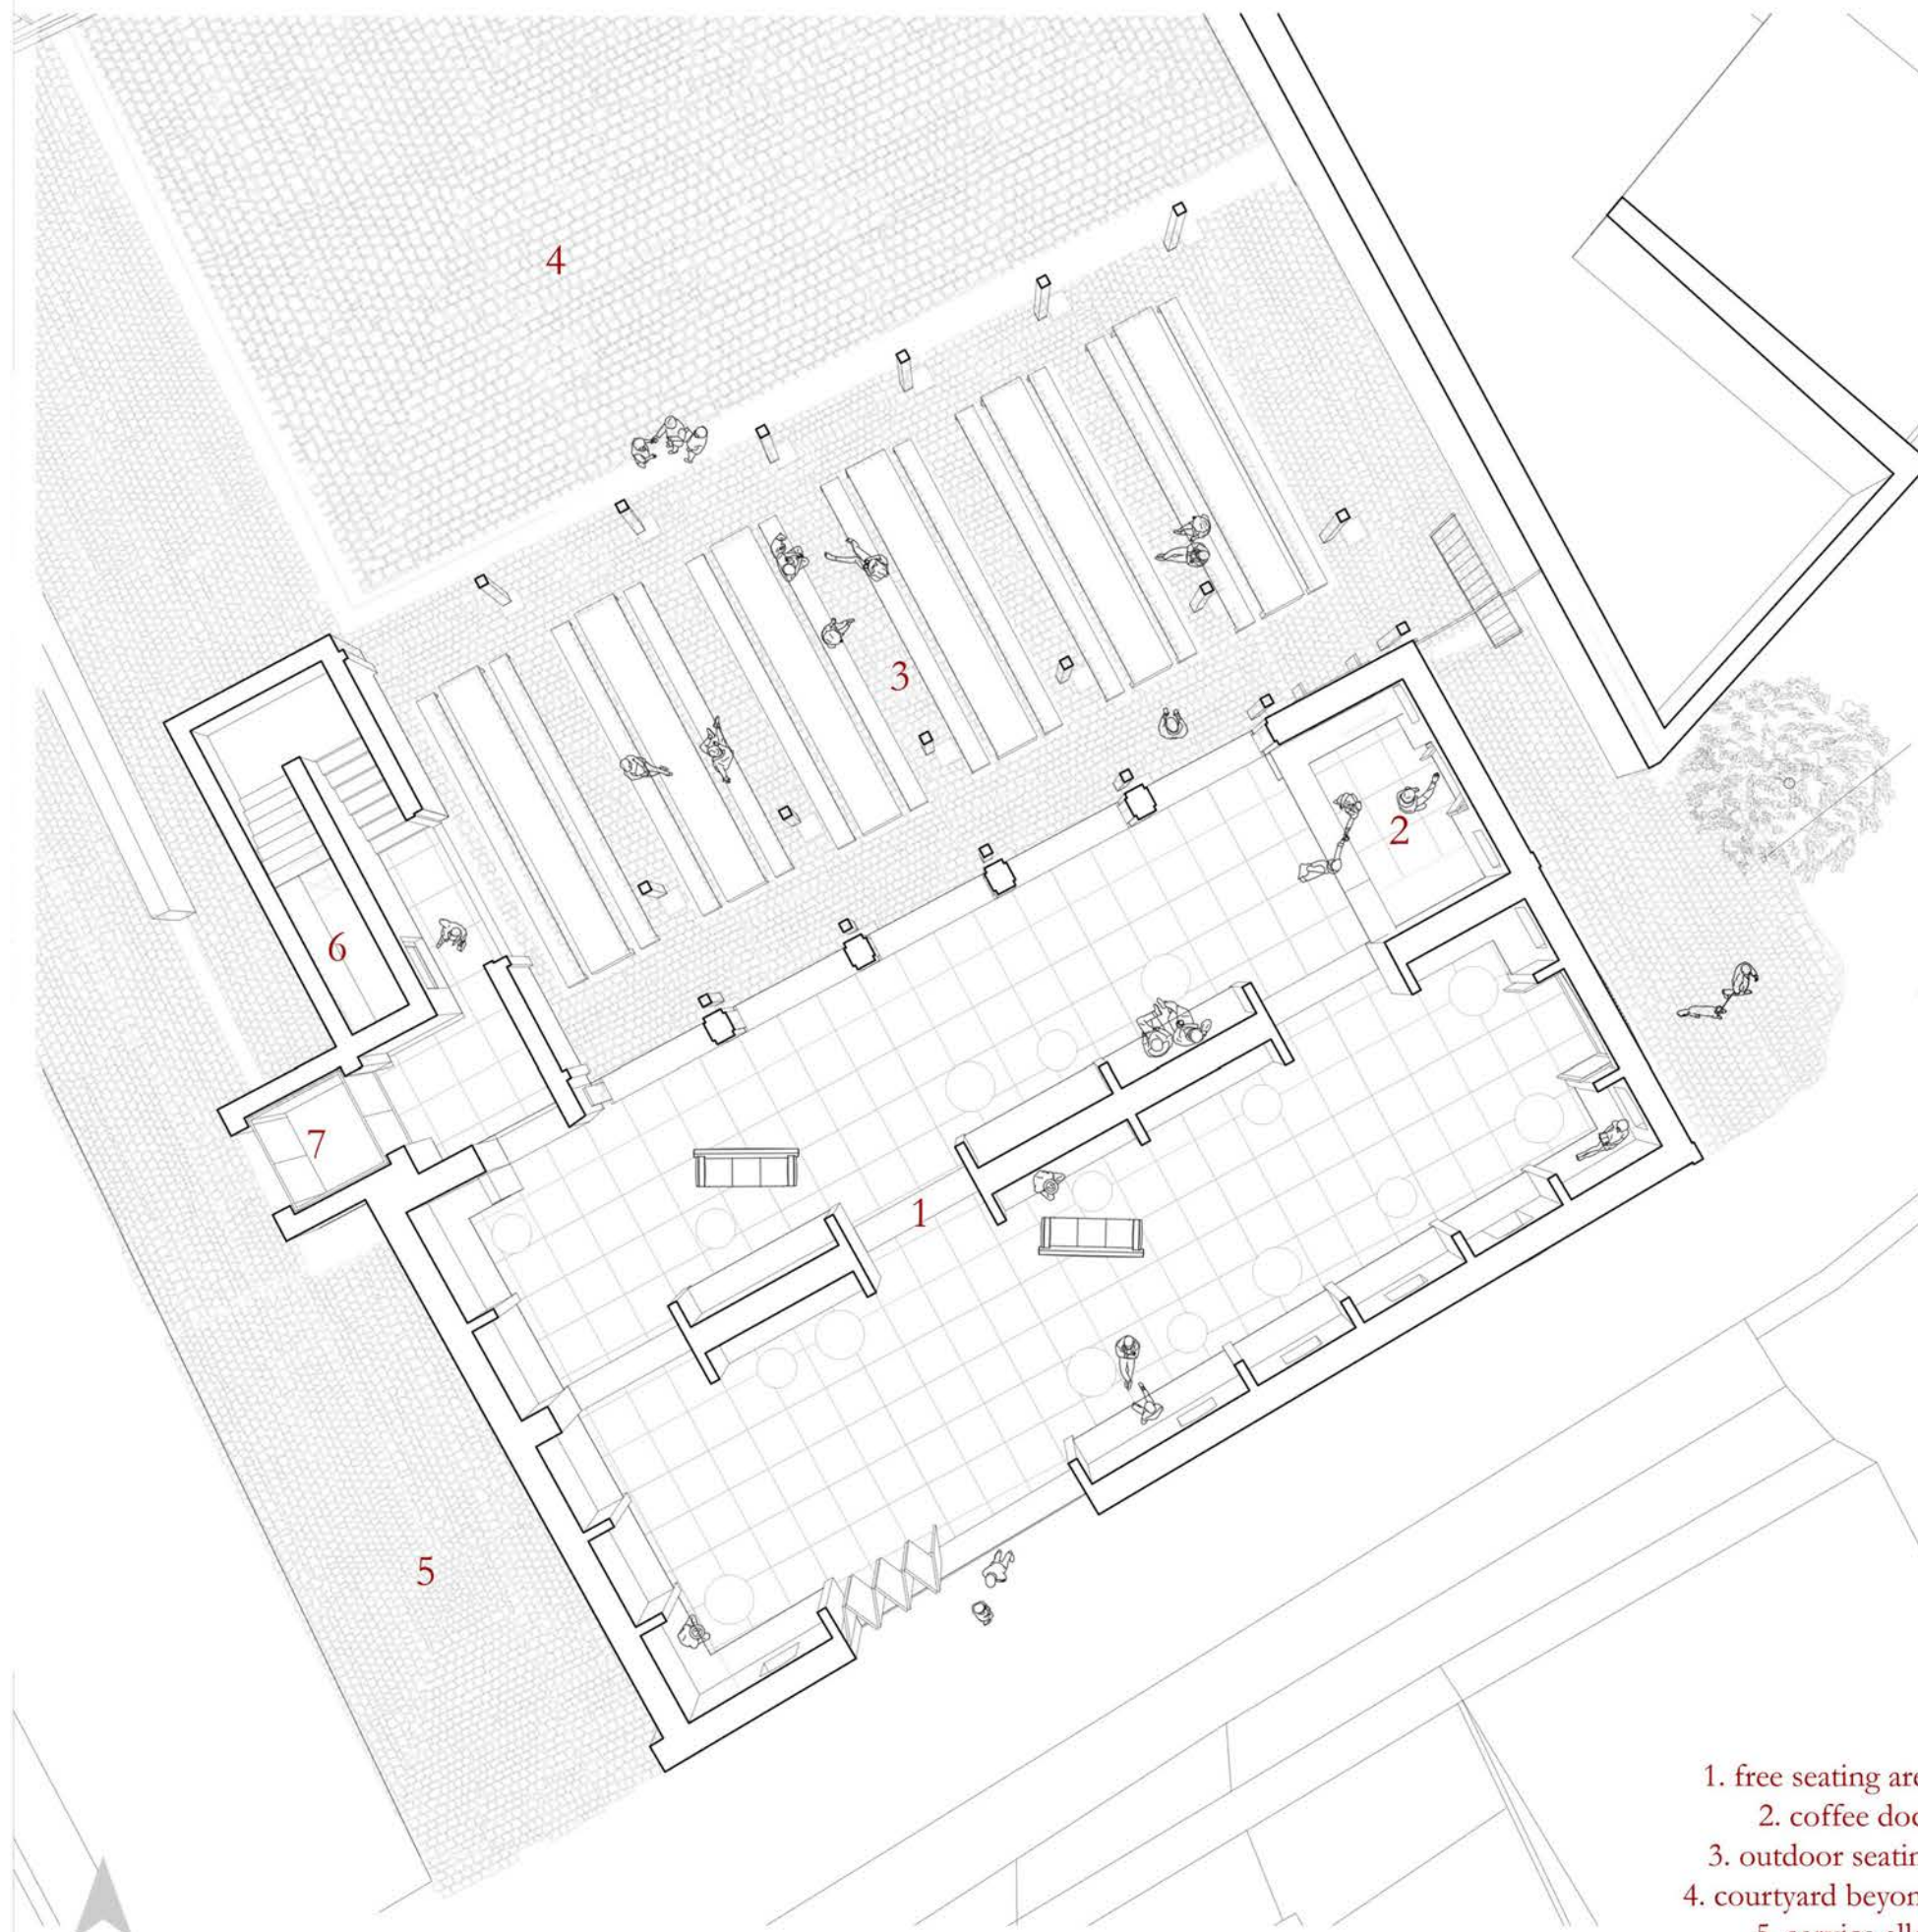

perspectival plan of 'cistin' a meeting place and interface with the city

learning from levis'


inhabited  
edge

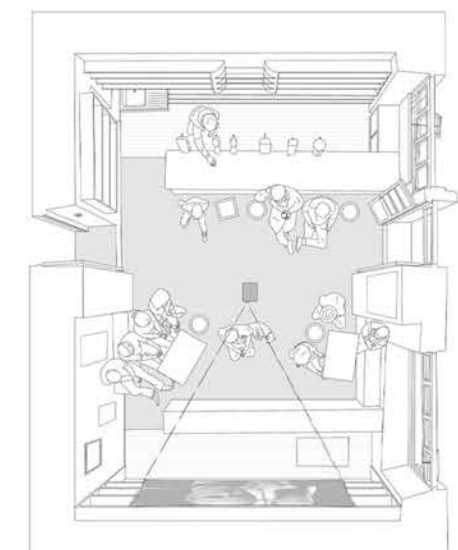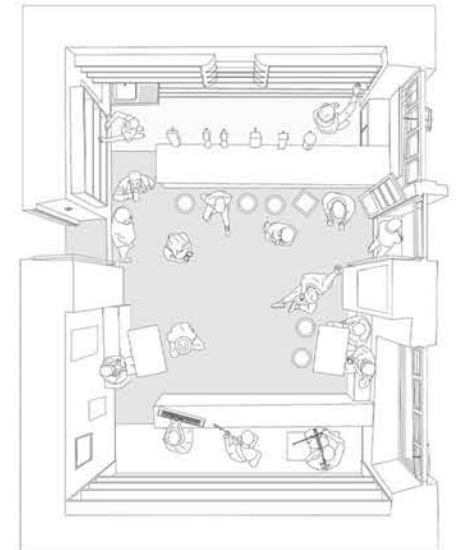

- 1. free seating area
- 2. coffee dock
- 3. outdoor seating
- 4. courtyard beyond
- 5. service alley
- 6. bathroom
- 7. lift




Learning From:  
 'The Hatch' in Levis' Cornerhouse, traditionally  
 allowing workers from the forge to get served  
 without entering the bar

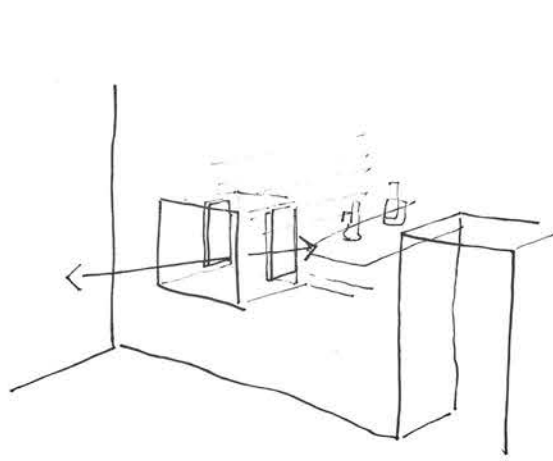

'Its all about meeting people,  
 that's what its about like,  
 meeting and contact and socialising like.  
 Its not about drink;  
 its conversations and its just  
 having a chat.  
 And three simple words; 'are you okay?'  
 And you know people need to hear that like,  
 its part of the pub business'


- RTÉ radio documentary on Levis' Cornerhouse

Learning From:  
 Cork sculptor Séamus Murphy's dog friendly  
 stonework on Patrick's Street.

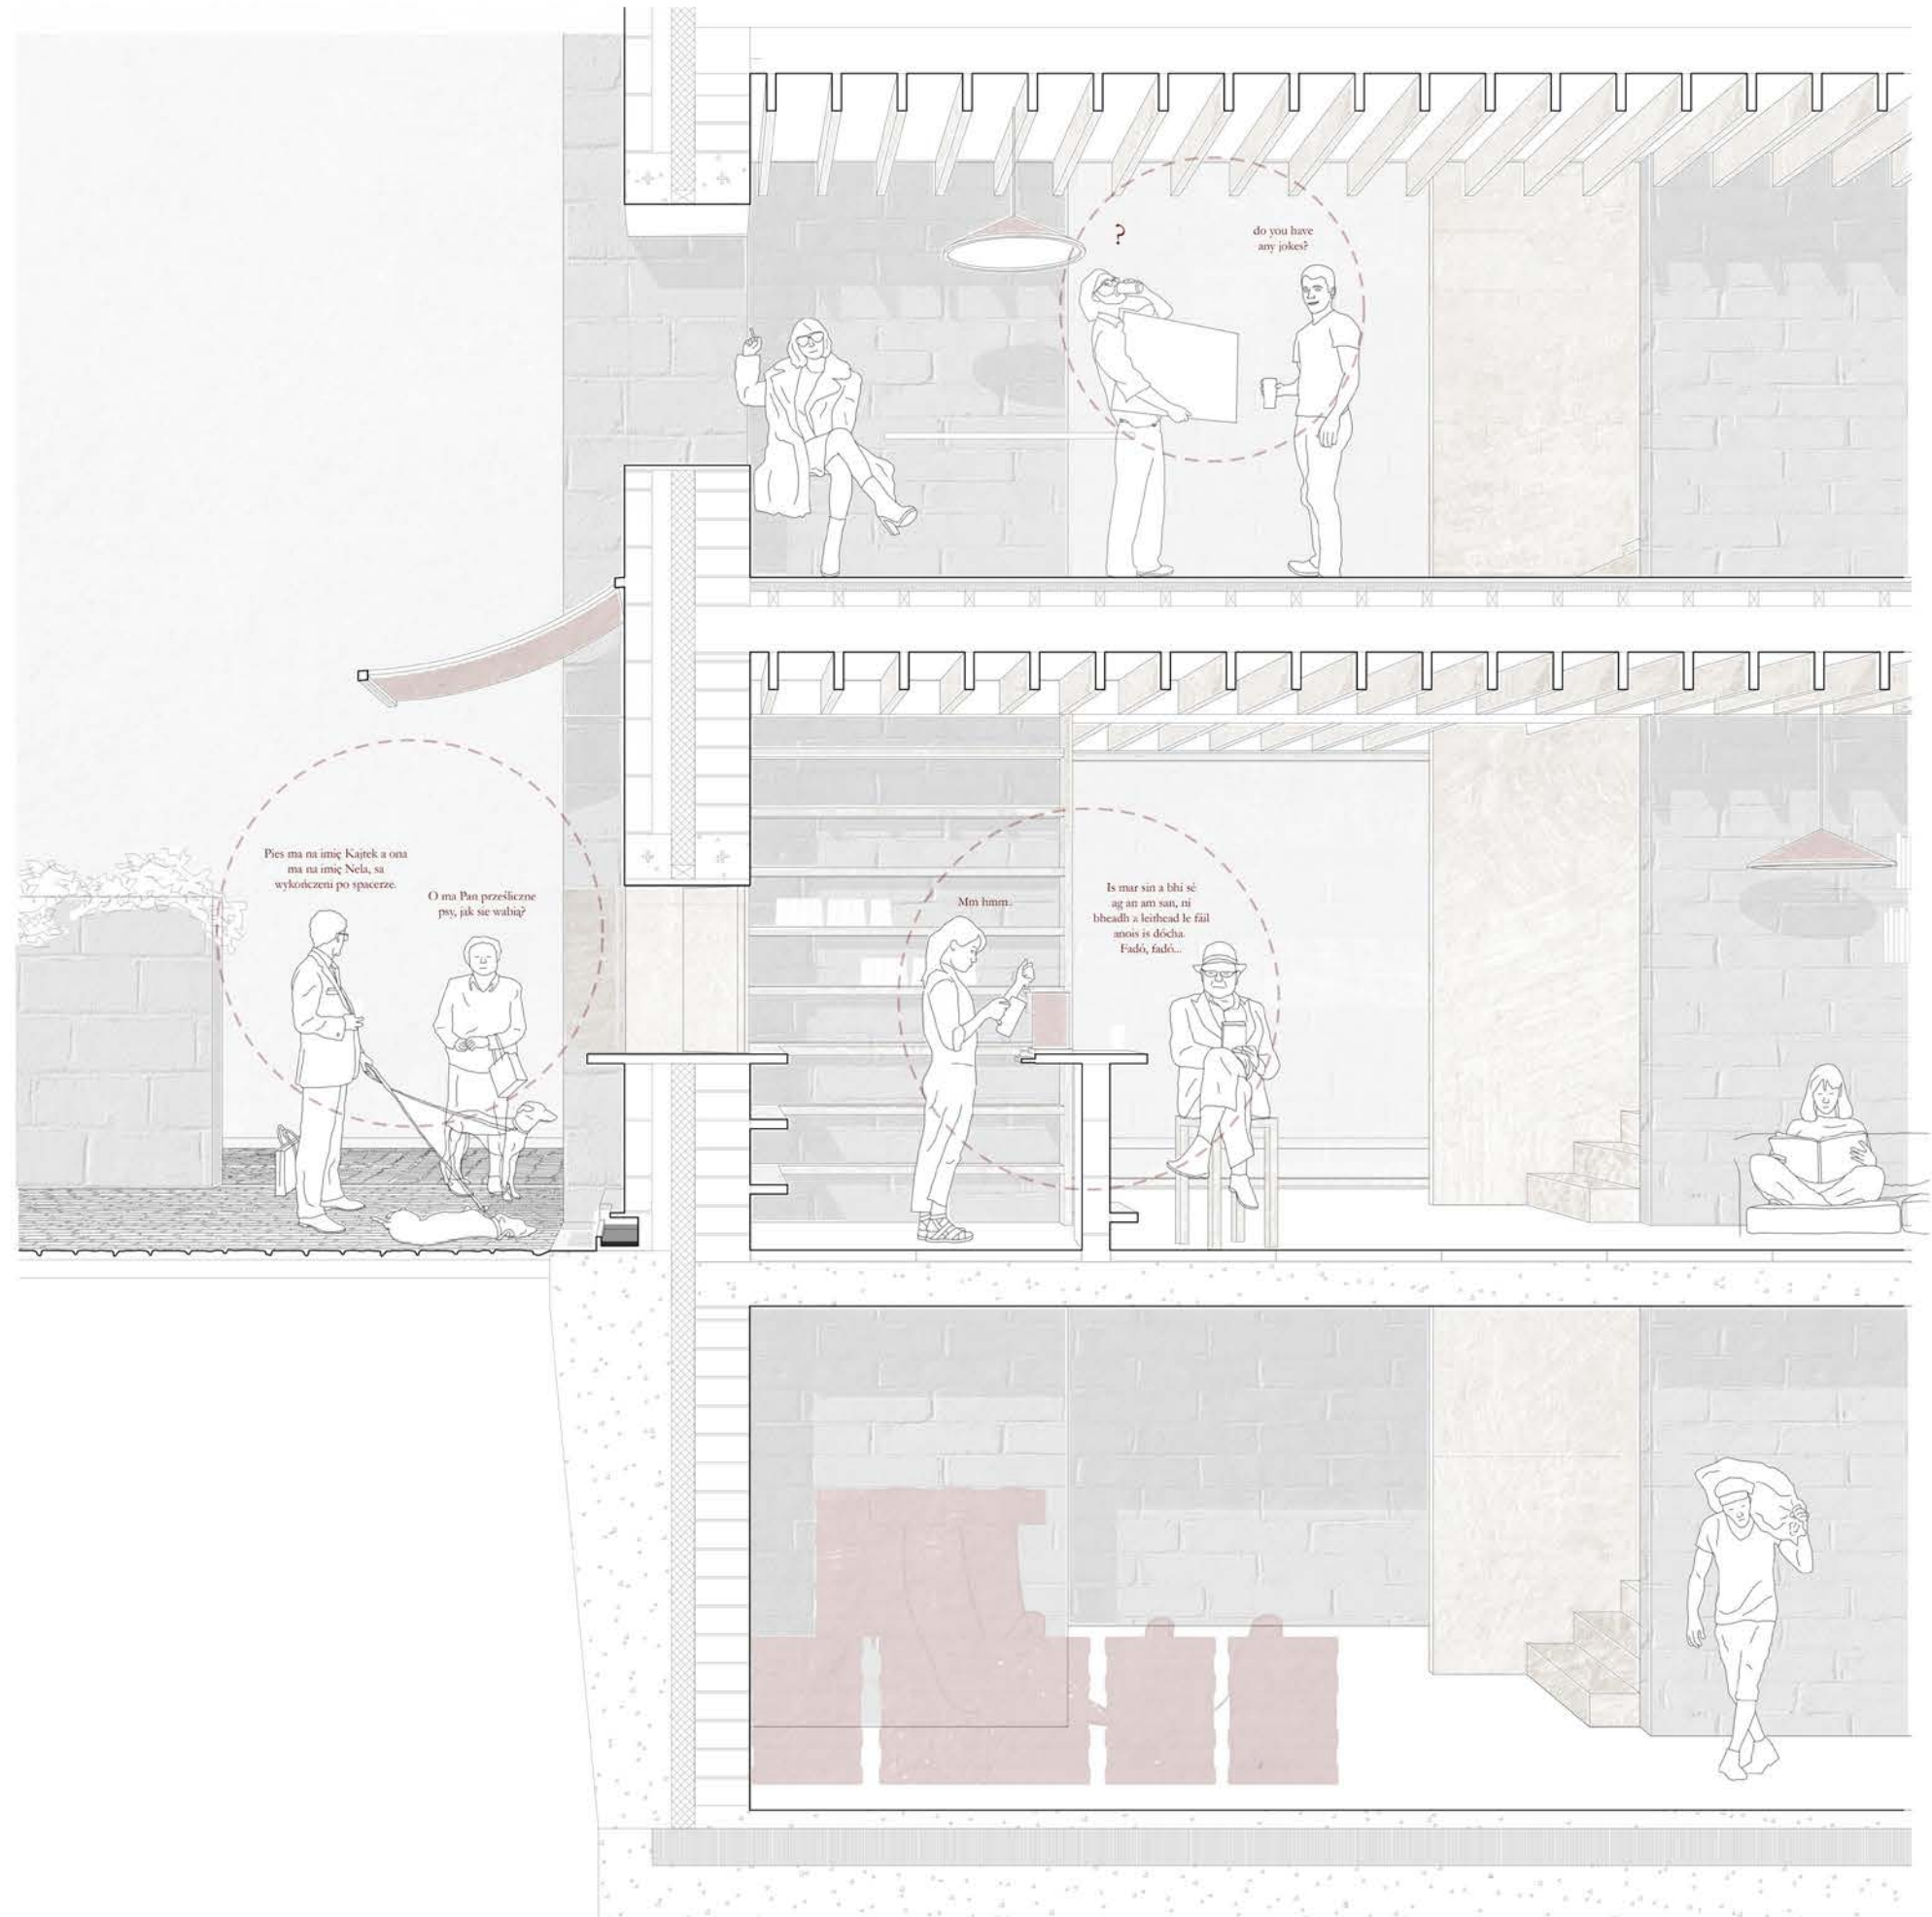

section showing construction and social context



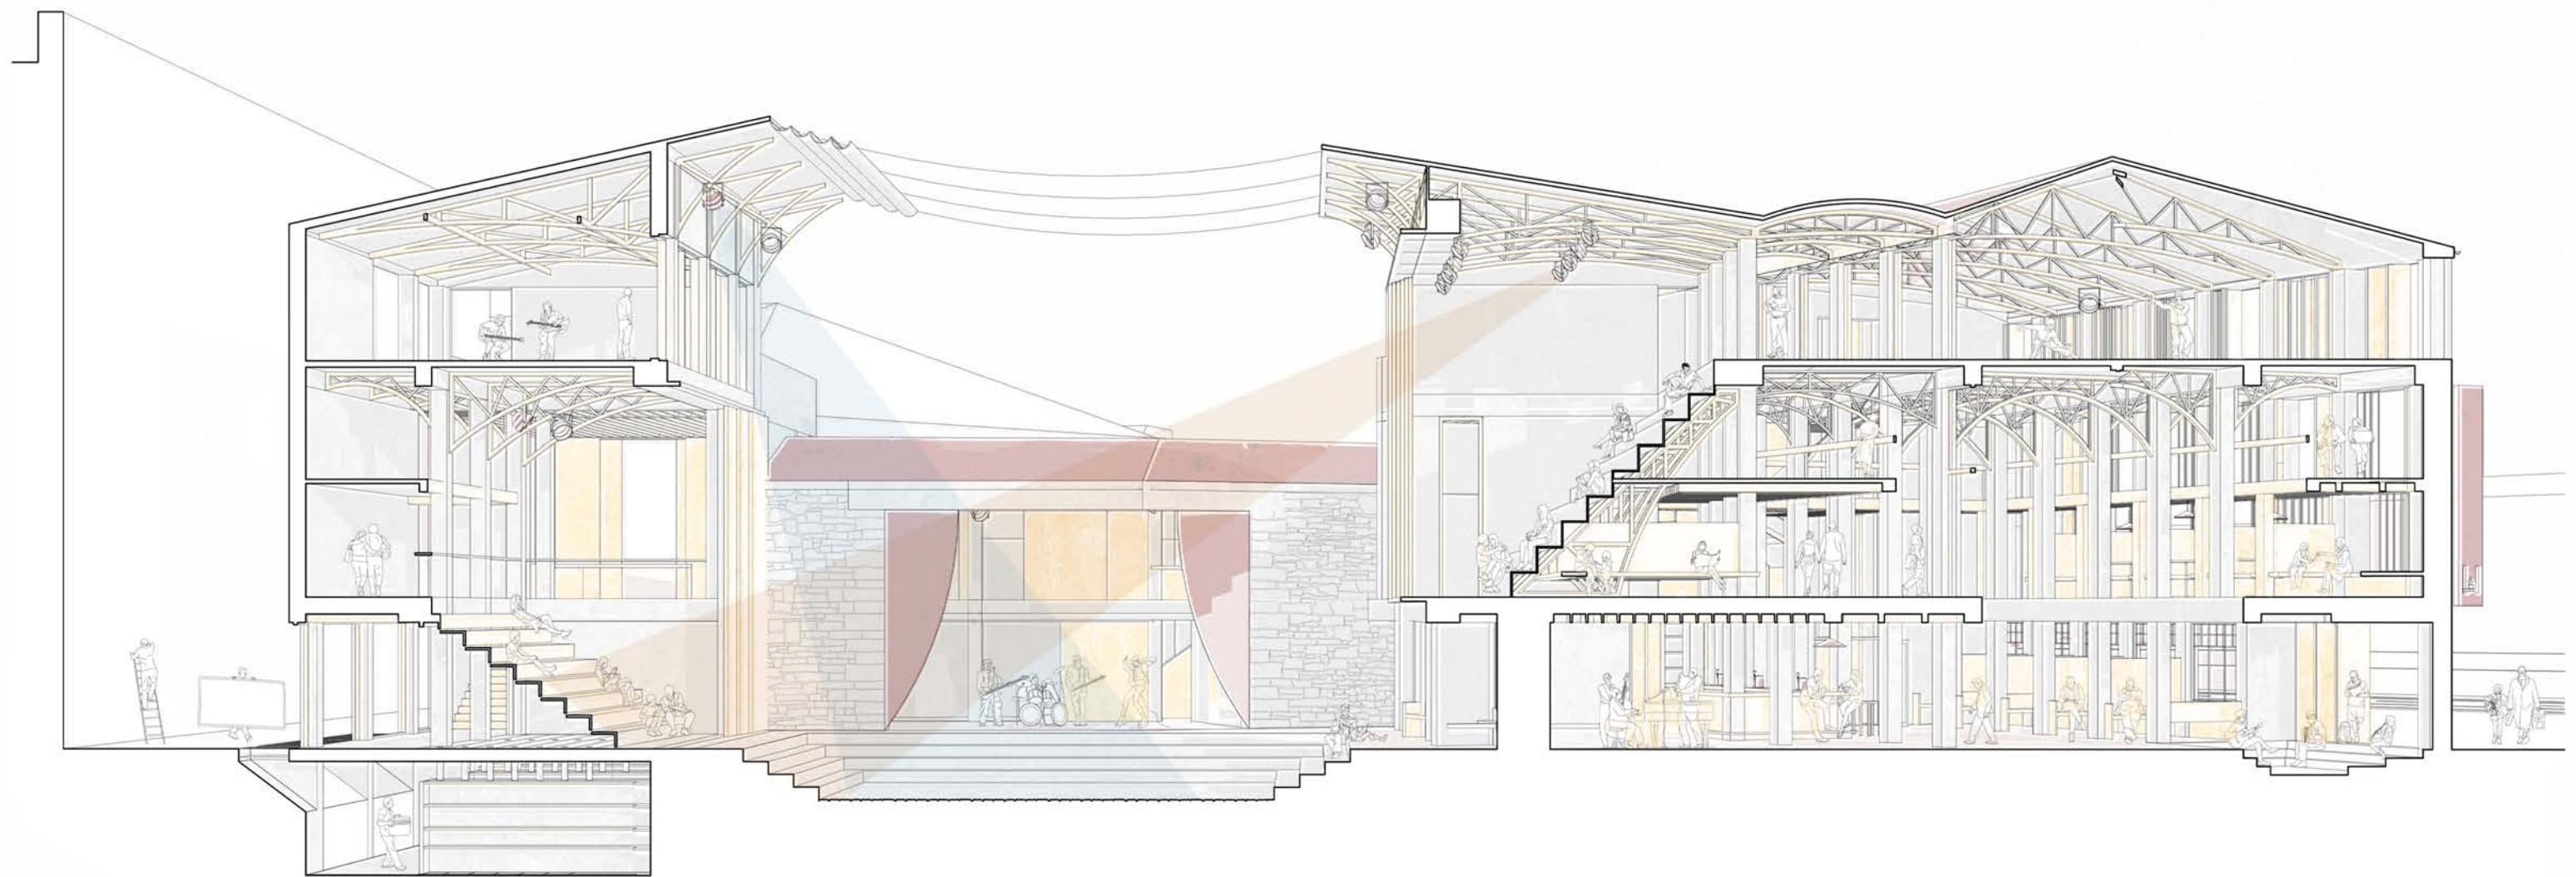

section cut 'north-south' through scheme, facing west



THANK YOU GO RAIBH MAITH AGAT

I appreciate the time you have taken to look through this portfolio.